

บริษัท เจ-สัน คอนสตรัคชั่น (ประเทศไทย) จำกัด
J-SONS CONSTRUCTION (THAILAND) COMPANY LIMITED
193/36-37 ถนนพหลโยธิน แขวงจตุจักร เขตจตุจักร กรุงเทพฯ 10130
Tel. (053) 214963 Fax. (053) 219842

ASBULT DRAWING

สถาปัตยวิธานและแปลนอาคาร
คณะวิศวกรของบริษัท
มหาวิทยาลัยเทคโนโลยีพระจอมเกล้าธนบุรี

OWNER

คณะวิศวกรรมศาสตร์ มหาวิทยาลัยเทคโนโลยีพระจอมเกล้าธนบุรี

ARCHITECTS

เขียน ธีรพัฒน์ งาม 82 ๑

STRUCTURAL ENGINEERS

บุญชัย พันธ์พชรกุล งาม 16450

SANITARY ENGINEERS

จุฬาลงกรณ์มหาวิทยาลัย งาม 18024

ELECTRICAL ENGINEERS

เอกา ภัทระพงศ์ งาม 828
เกษม งาม 20108

MECHANICAL ENGINEERS

ณัฏฐ์ ธีรพัฒน์ งาม 8137

DRAWN

ธีรพัฒน์ งาม

SHEET TITLE

ELECTRICAL SYSTEM
LAYOUT ON 4TH FLOOR (FLOOR PLAN)

SCALE : AS SHOWN


DATE : 2 พฤษภาคม 2542

APPROVED :

DATE :

DRAWING NO. TOTAL SHEET

EE-20 46

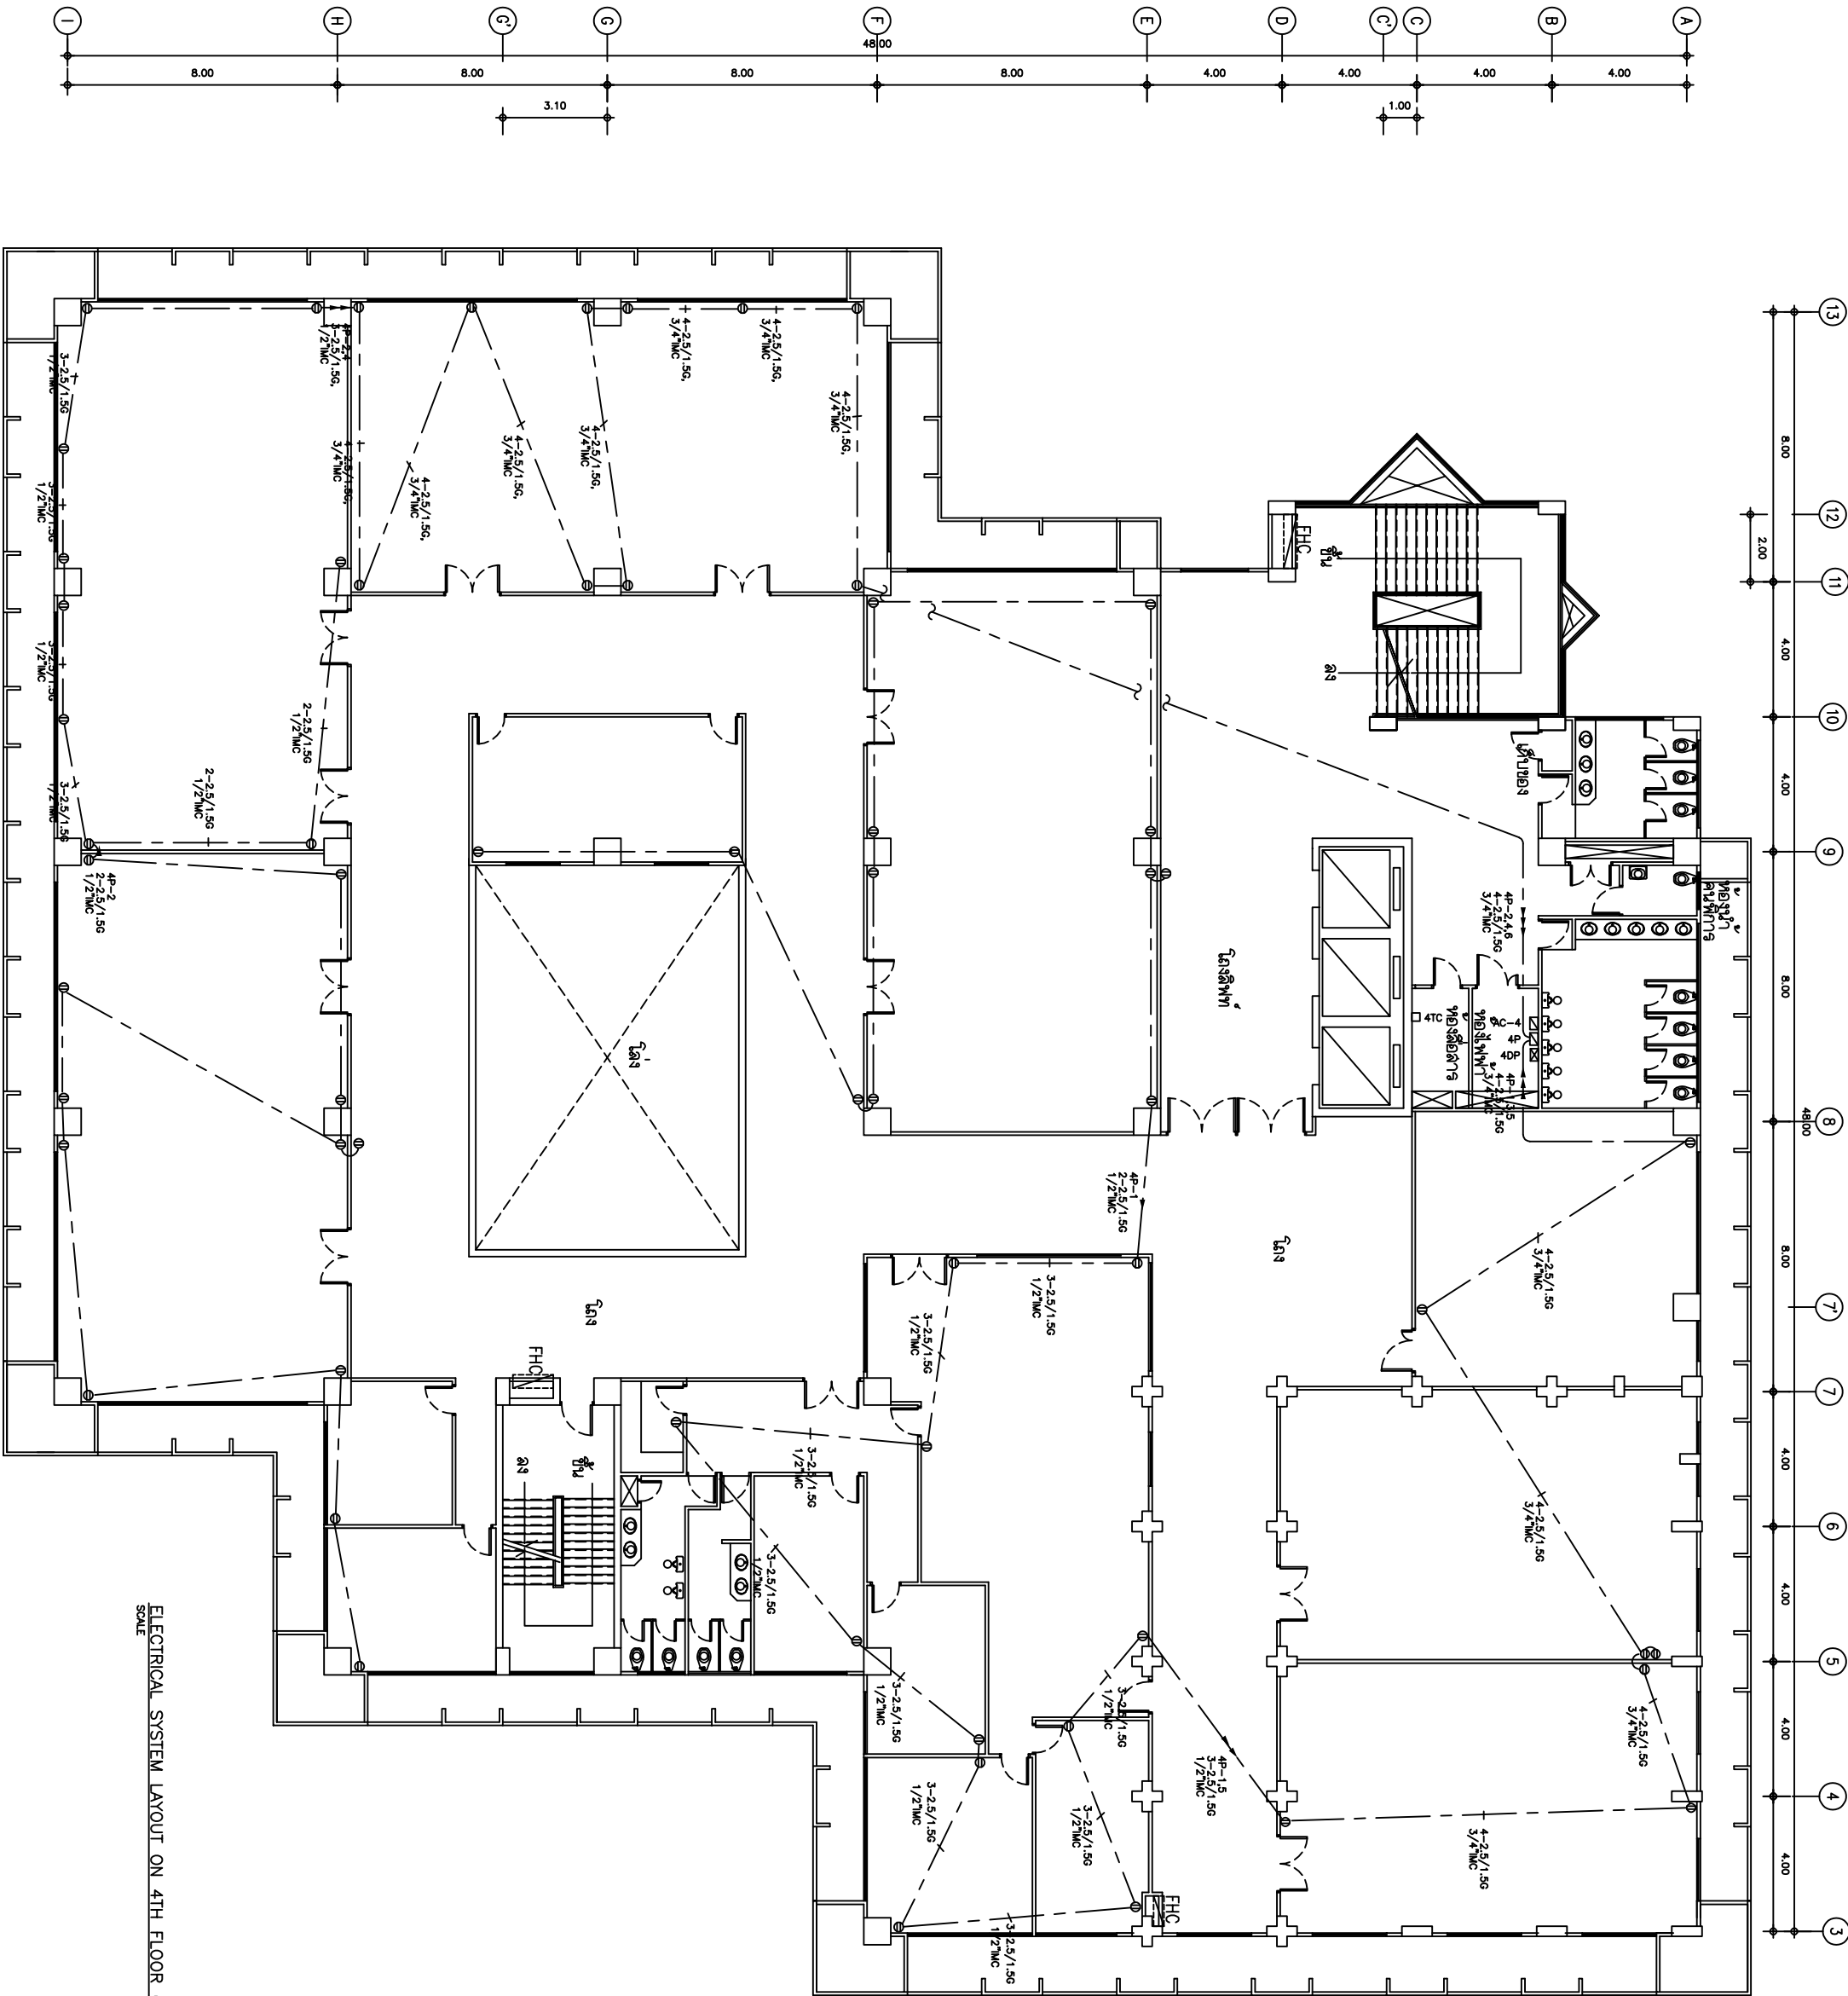

ELECTRICAL SYSTEM LAYOUT ON 4TH FLOOR (FLOOR PLAN)
SCALE 1:100