

บริษัท เจ-สัน คอนสตรัคชั่น (ประเทศไทย) จำกัด
J-SONS CONSTRUCTION (THAILAND) COMPANY LIMITED
193/36-37 ถนนพหลโยธิน กรุงเทพมหานคร 10330
Tel. (053) 214963 Fax. (053) 219842

ASBULT DRAWING

สถาปนาริเสนแบบและปฏิบัติงานการ
ออกแบบวิศวกรรมศาสตาร
มหาวิทยาลัยมหิดลพิษณุพน

OWNER

คณะวิศวกรรมศาสตร มหาวิทยาลัยมหิดลพิษณุพน

ARCHITECTS

เสพน ธีรภณพท ๓๓. ๑2 ฉ

STRUCTURAL ENGINEERS

เบญชัย พธิ์พวธิ์สิน ๓๒. 16450

SANITARY ENGINEERS

จตุภพ ศัยพวธิ์สิน ๓๒. 18024

ELECTRICAL ENGINEERS

เอกา ภัทธิพพท ๓๓๓. 828
กฤษณะ ธีนดี ๓๓๓. 20108

MECHANICAL ENGINEERS

ฉนศัณ ธีนพพท ๓๓. 8137

DRAWN

วิระพพท ธีนพ

SHEET TITLE

ELECTRICAL SYSTEM
LAYOUT ON 6TH FLOOR (FLOOR PLAN)

SCALE : AS SHOWN


DATE : 2 พธิ์พทพ 2542

APPROVED :

DATE :

DRAWING NO. TOTAL SHEET

EE-30 46

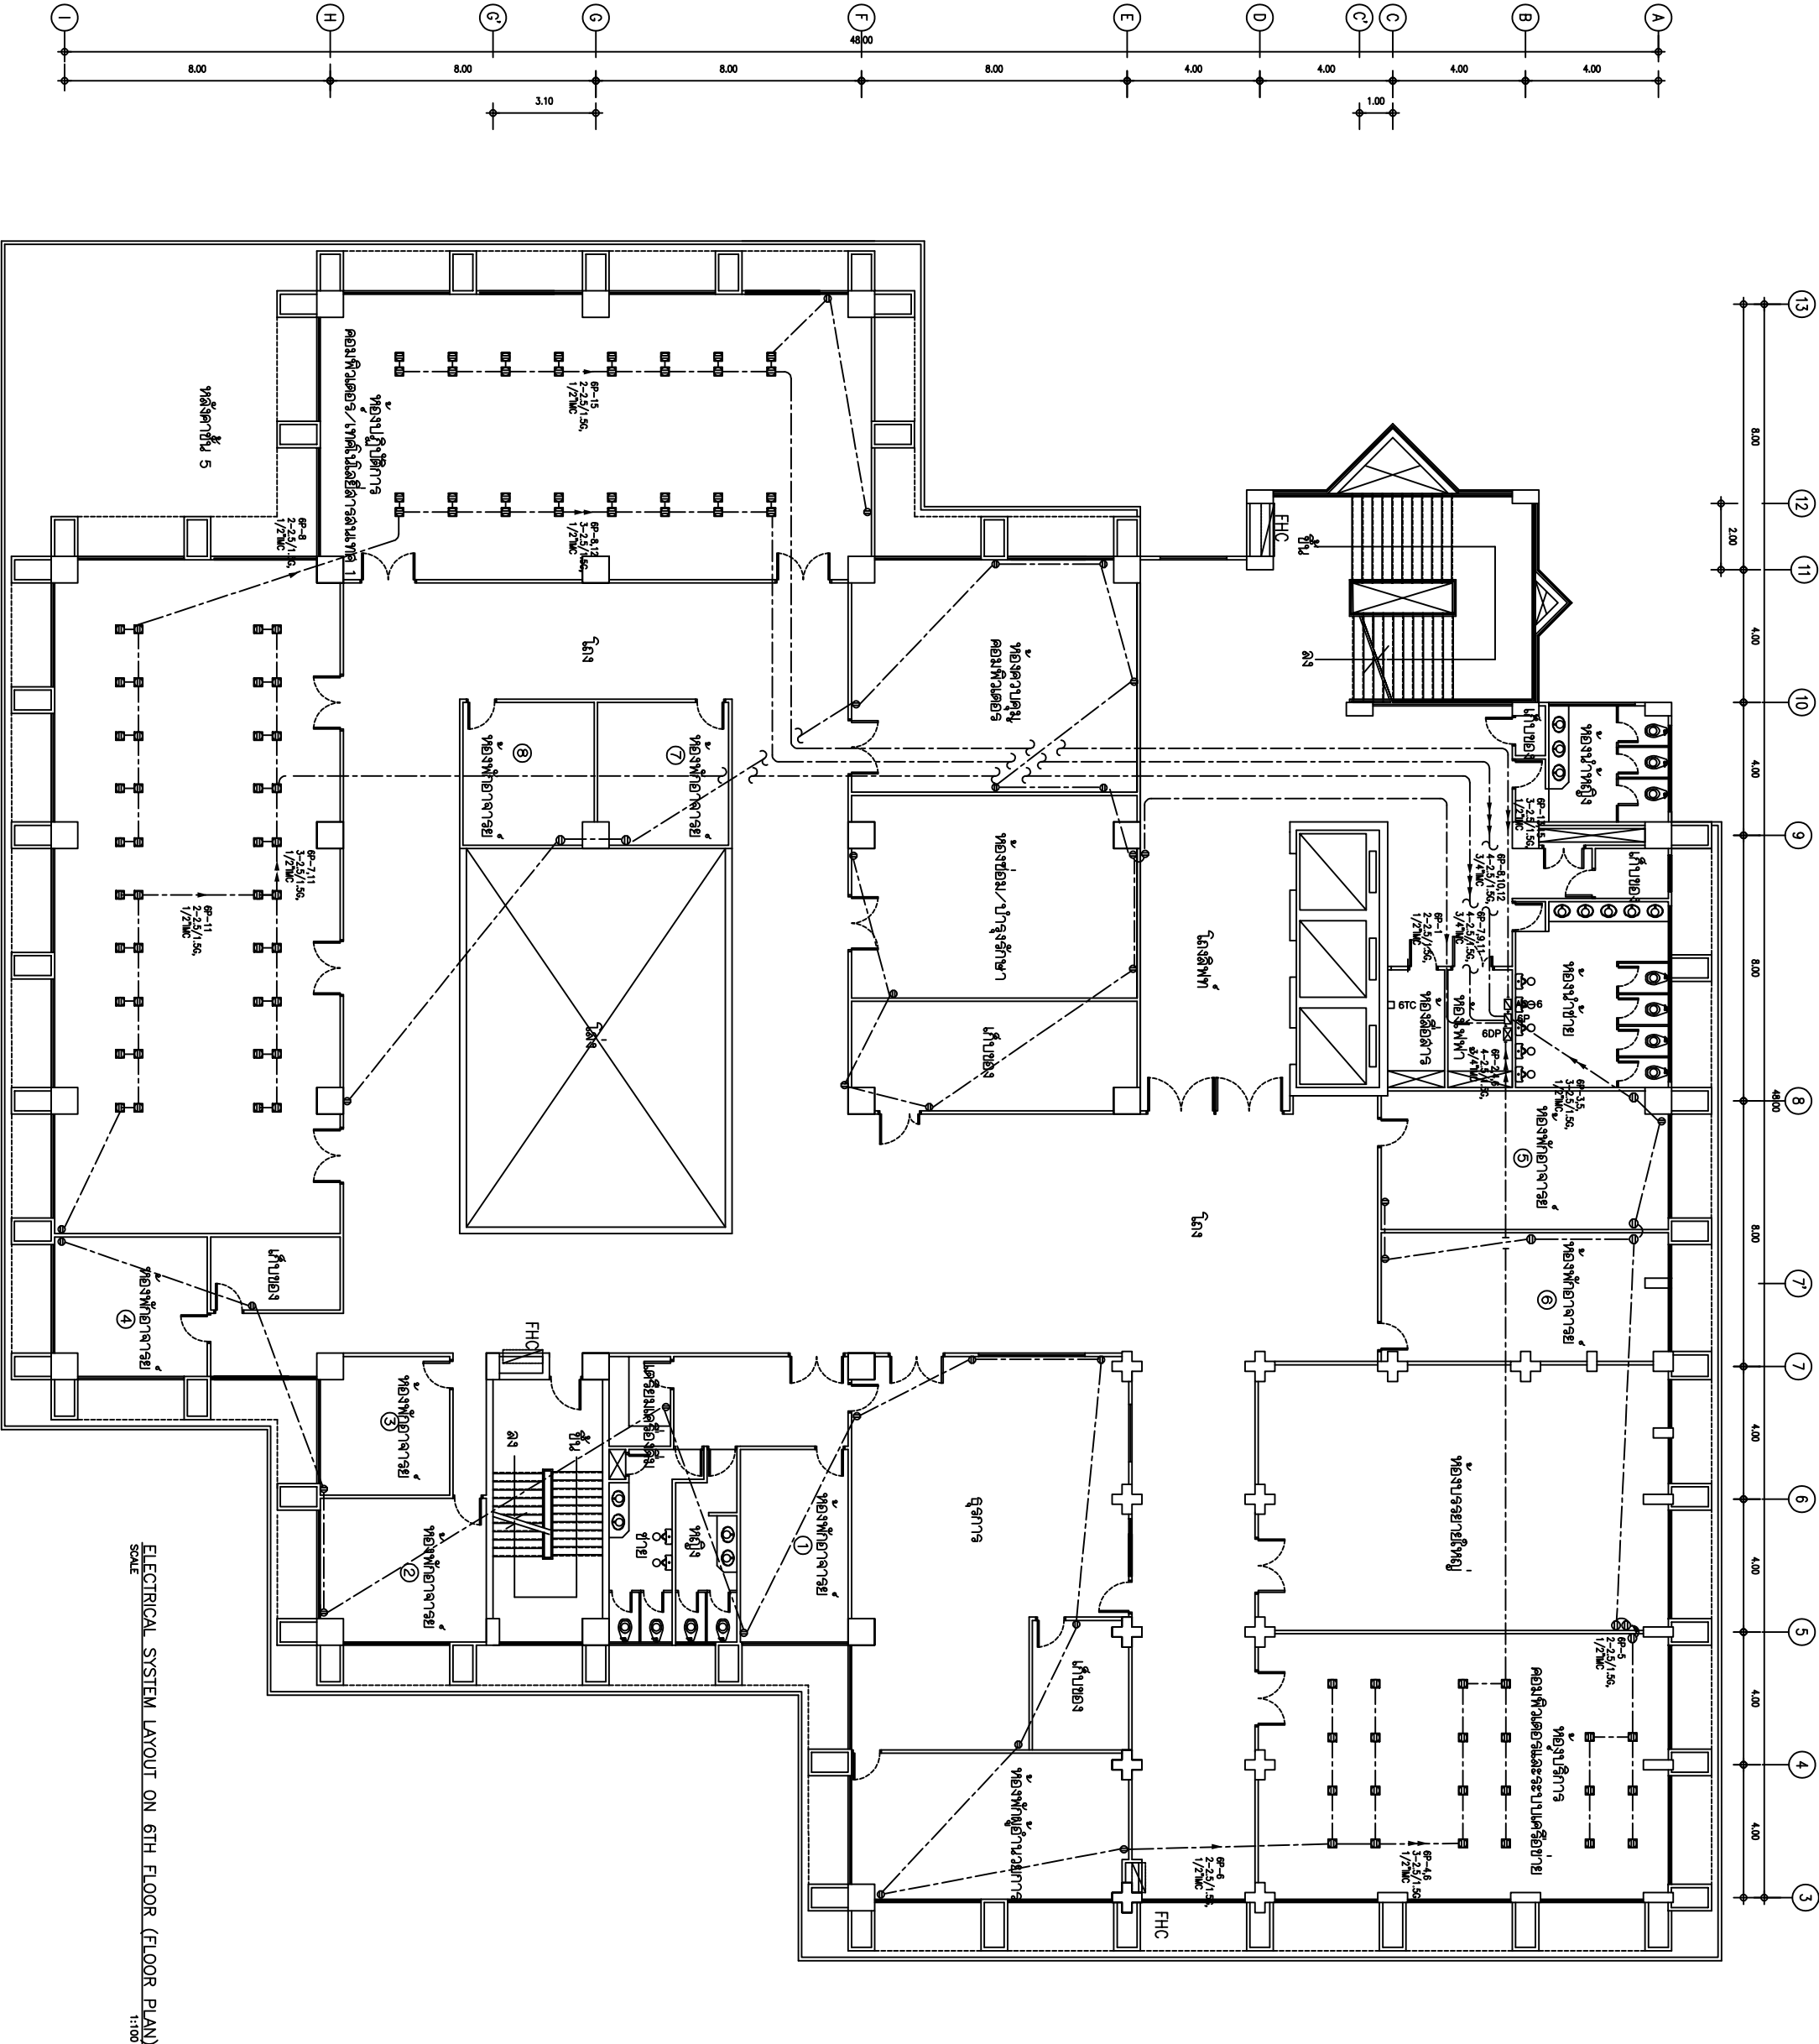

ELECTRICAL SYSTEM LAYOUT ON 6TH FLOOR (FLOOR PLAN)
1:100