

บริษัท เอ-สัน คอนสตรัคชั่น (ประเทศไทย) จำกัด
J-SONS CONSTRUCTION (THAILAND) COMPANY LIMITED
193/36-37 ถนนพหลโยธิน แขวงจตุจักร เขตจตุจักร กรุงเทพฯ 10130
Tel. (053) 2149653 Fax. (053) 219842

ASBULT DRAWING

อาคารพาณิชย์บนถนนพหลโยธิน
คณะวิศวกรรมศาสตรบัณฑิต
มหาวิทยาลัยเทคโนโลยีพระจอมเกล้าธนบุรี

OWNER

คณะวิศวกรรมศาสตรบัณฑิต มหาวิทยาลัยเทคโนโลยีพระจอมเกล้าธนบุรี

ARCHITECTS

เขียน สถาปนิก อด. 82 ฉ

STRUCTURAL ENGINEERS

เขียน วิศวกรโยธา งบ. 16450

SANITARY ENGINEERS

เขียน วิศวกรโยธา งบ. 16024

ELECTRICAL ENGINEERS

เขียน วิศวกรโยธา งบ. 828
เขียน วิศวกรโยธา งบ. 20108

MECHANICAL ENGINEERS

เขียน วิศวกรโยธา งบ. 8137

DRAWN

เขียน วิศวกรโยธา

SHEET TITLE

ELECTRICAL SYSTEM
LAYOUT ON 7TH FLOOR (FLOOR PLAN)

SCALE : AS SHOWN


DATE : 2 พฤษภาคม 2542

APPROVED :

DATE :

DRAWING NO. TOTAL SHEET

EE-35 46

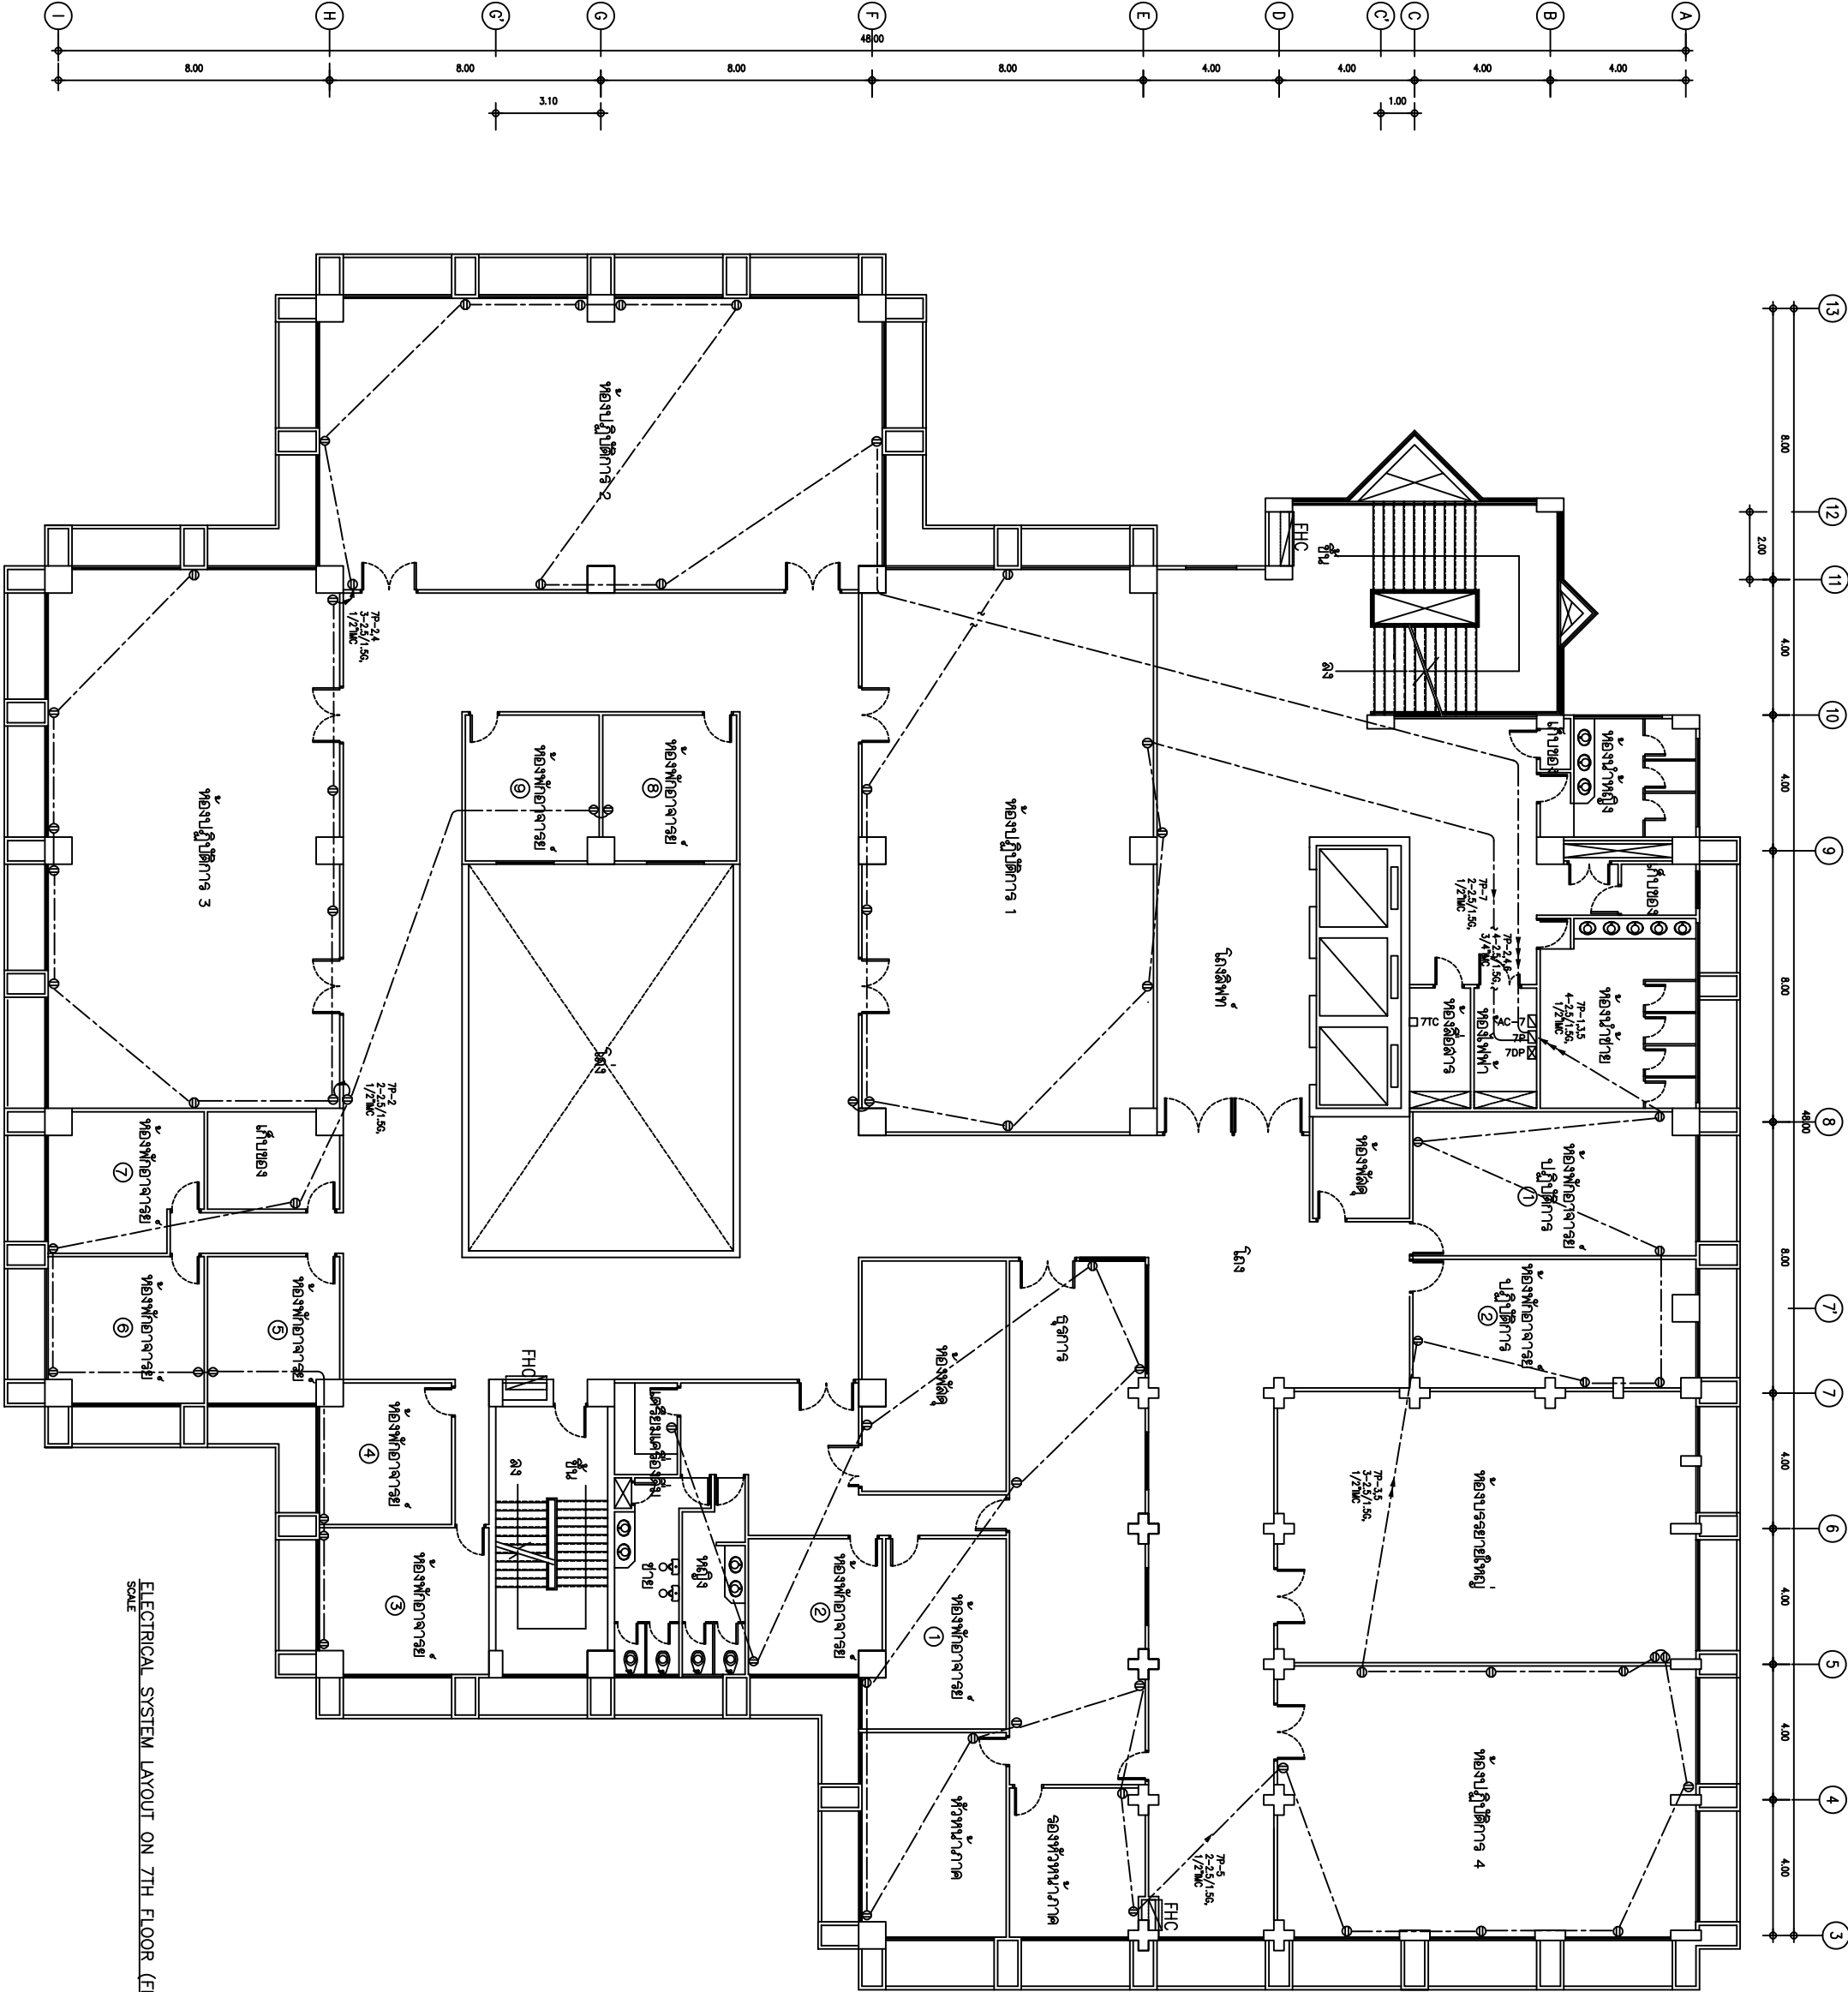

ELECTRICAL SYSTEM LAYOUT ON 7TH FLOOR (FLOOR PLAN)
1:100