

บริษัท เอ-สัน คอนสตรัคชั่น (ประเทศไทย) จำกัด
J-SONS CONSTRUCTION (THAILAND) COMPANY LIMITED
183/36-37 ถนนพหลโยธิน แขวงจตุจักร เขตจตุจักร กรุงเทพฯ 10130
Tel. (053) 214963 Fax. (053) 219842

ASBULT DRAWING

สถาปนิกชั้นบนและบันไดขึ้นอาคาร
คณะวิศวกรของบริษัท
มหาวิทยาลัยเทคโนโลยีพระจอมเกล้าธนบุรี

OWNER

คณะวิศวกรรมศาสตร์ มหาวิทยาลัยเทคโนโลยีพระจอมเกล้าธนบุรี

ARCHITECTS

เขียน ธีรพัฒน์ งาม 82 ส

STRUCTURAL ENGINEERS

เขียน ธีรพัฒน์ งาม 16450

SANITARY ENGINEERS

จตุพร ศรีงามศรี งาม 18024

ELECTRICAL ENGINEERS

เอกา ภัทริพงษ์ สก. 828
เกษม ธีรดี งาม 20108

MECHANICAL ENGINEERS

อัคริษฐ์ อัคริษฐ์ งาม 8137

DRAWN

ธีรพัฒน์ งาม

SHEET TITLE

แปลนชั้น 2-3

SCALE : AS SHOWN


DATE : 27 JANUARY 2542

APPROVED :

DATE :

DRAWING NO. TOTAL SHEET

AC-10 18

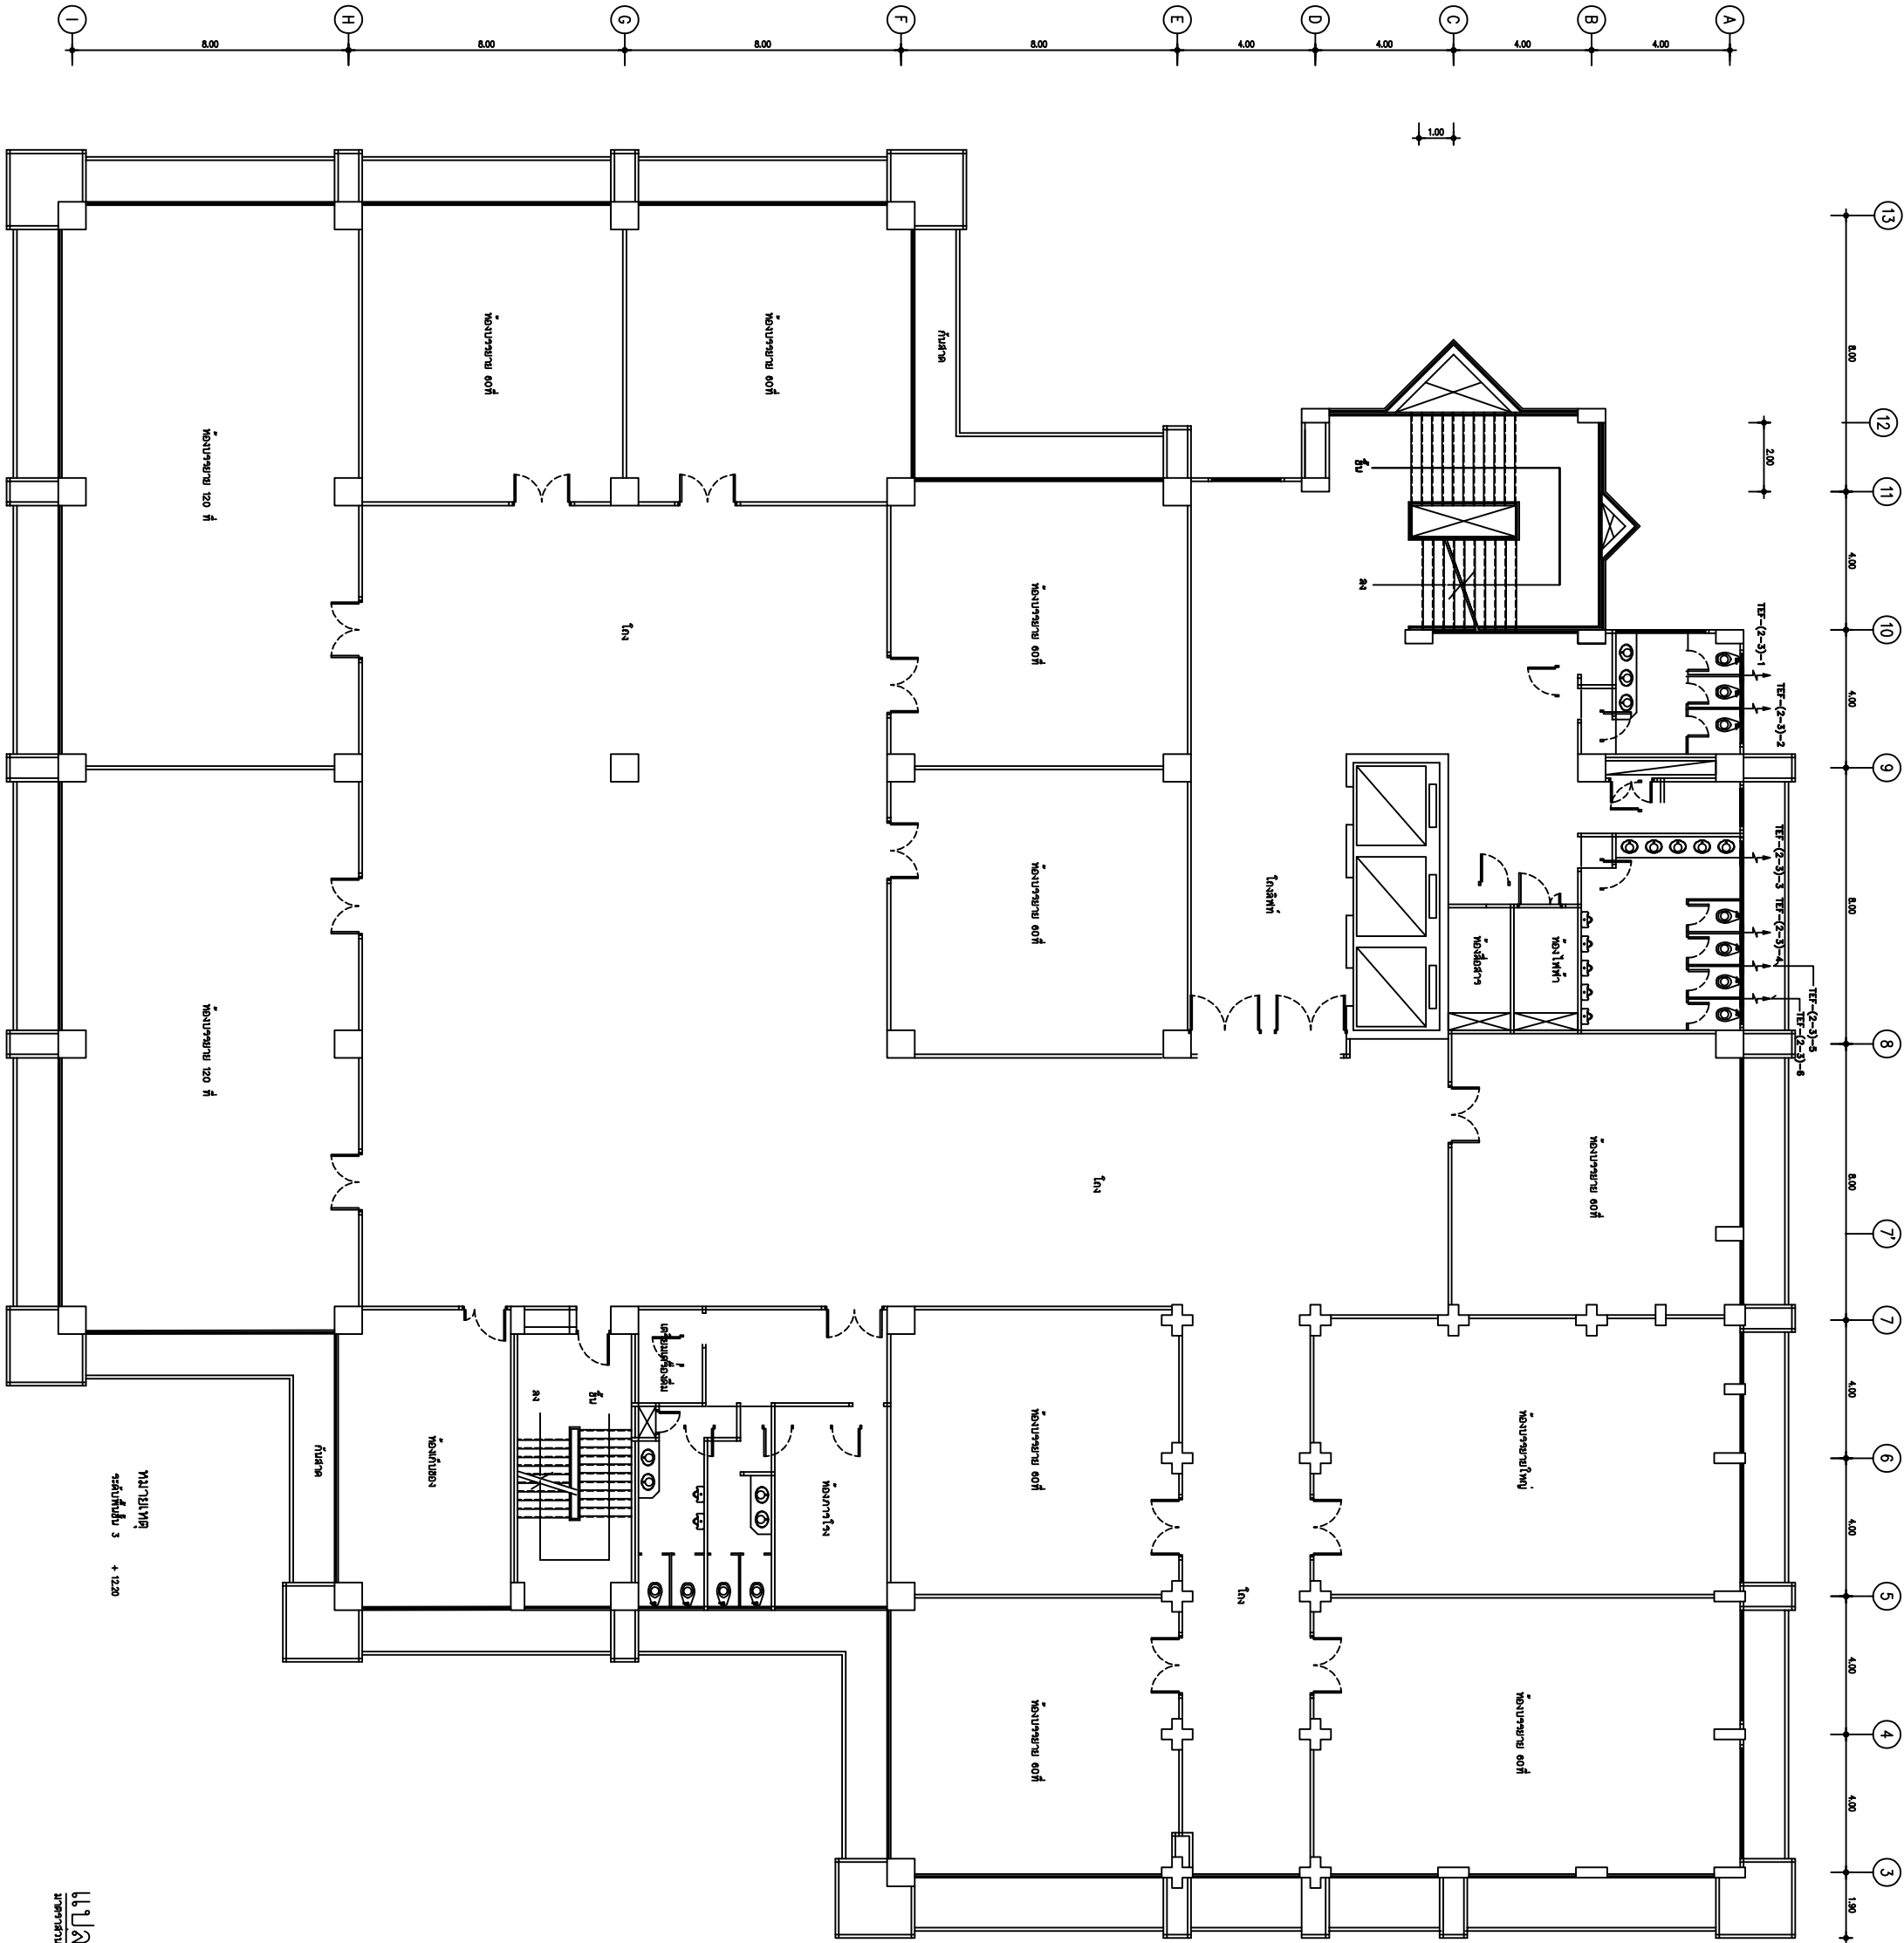

แปลนชั้น 2-3
1 : 100