

บริษัท เอ-สัน คอนสตรัคชั่น (ประเทศไทย) จำกัด
J-SONS CONSTRUCTION (THAILAND) COMPANY LIMITED
193/36-37 ถนนพหลโยธิน แขวงจตุจักร เขตจตุจักร กรุงเทพฯ 10130
Tel. (053) 214963 Fax. (053) 219842

ASBULT DRAWING

สถาปนาริเสนแบบและปฏิบัติงานการ
ออกแบบและวางระบบการระบายน้ำ
นพการิสถาปนาริเสนแบบและวางระบบ

OWNER

คณะบริหารการและการจัดการ มหาวิทยาลัยเทคโนโลยีพระจอมเกล้าธนบุรี

ARCHITECTS

เสถียร สถาปนาริเสนแบบ 20, 82 2

STRUCTURAL ENGINEERS

บุญชัย ทรัพย์เจริญ 70, 16450

SANITARY ENGINEERS

จตุพร ศิริยาเจริญ 70, 18024

ELECTRICAL ENGINEERS

เอกา ทรัพย์เจริญ 828
กฤษณะ ชินดี 70, 20108

MECHANICAL ENGINEERS

ฉัตรดี อธิปัตย์ 70, 8137

DRAWN

วิมลชัย ธรรมาน

SHEET TITLE

แบบแปลน 7

SCALE : AS SHOWN


DATE : 27 JANUARY 2542

APPROVED :

DATE :

DRAWING NO. TOTAL SHEET

AC-14 18

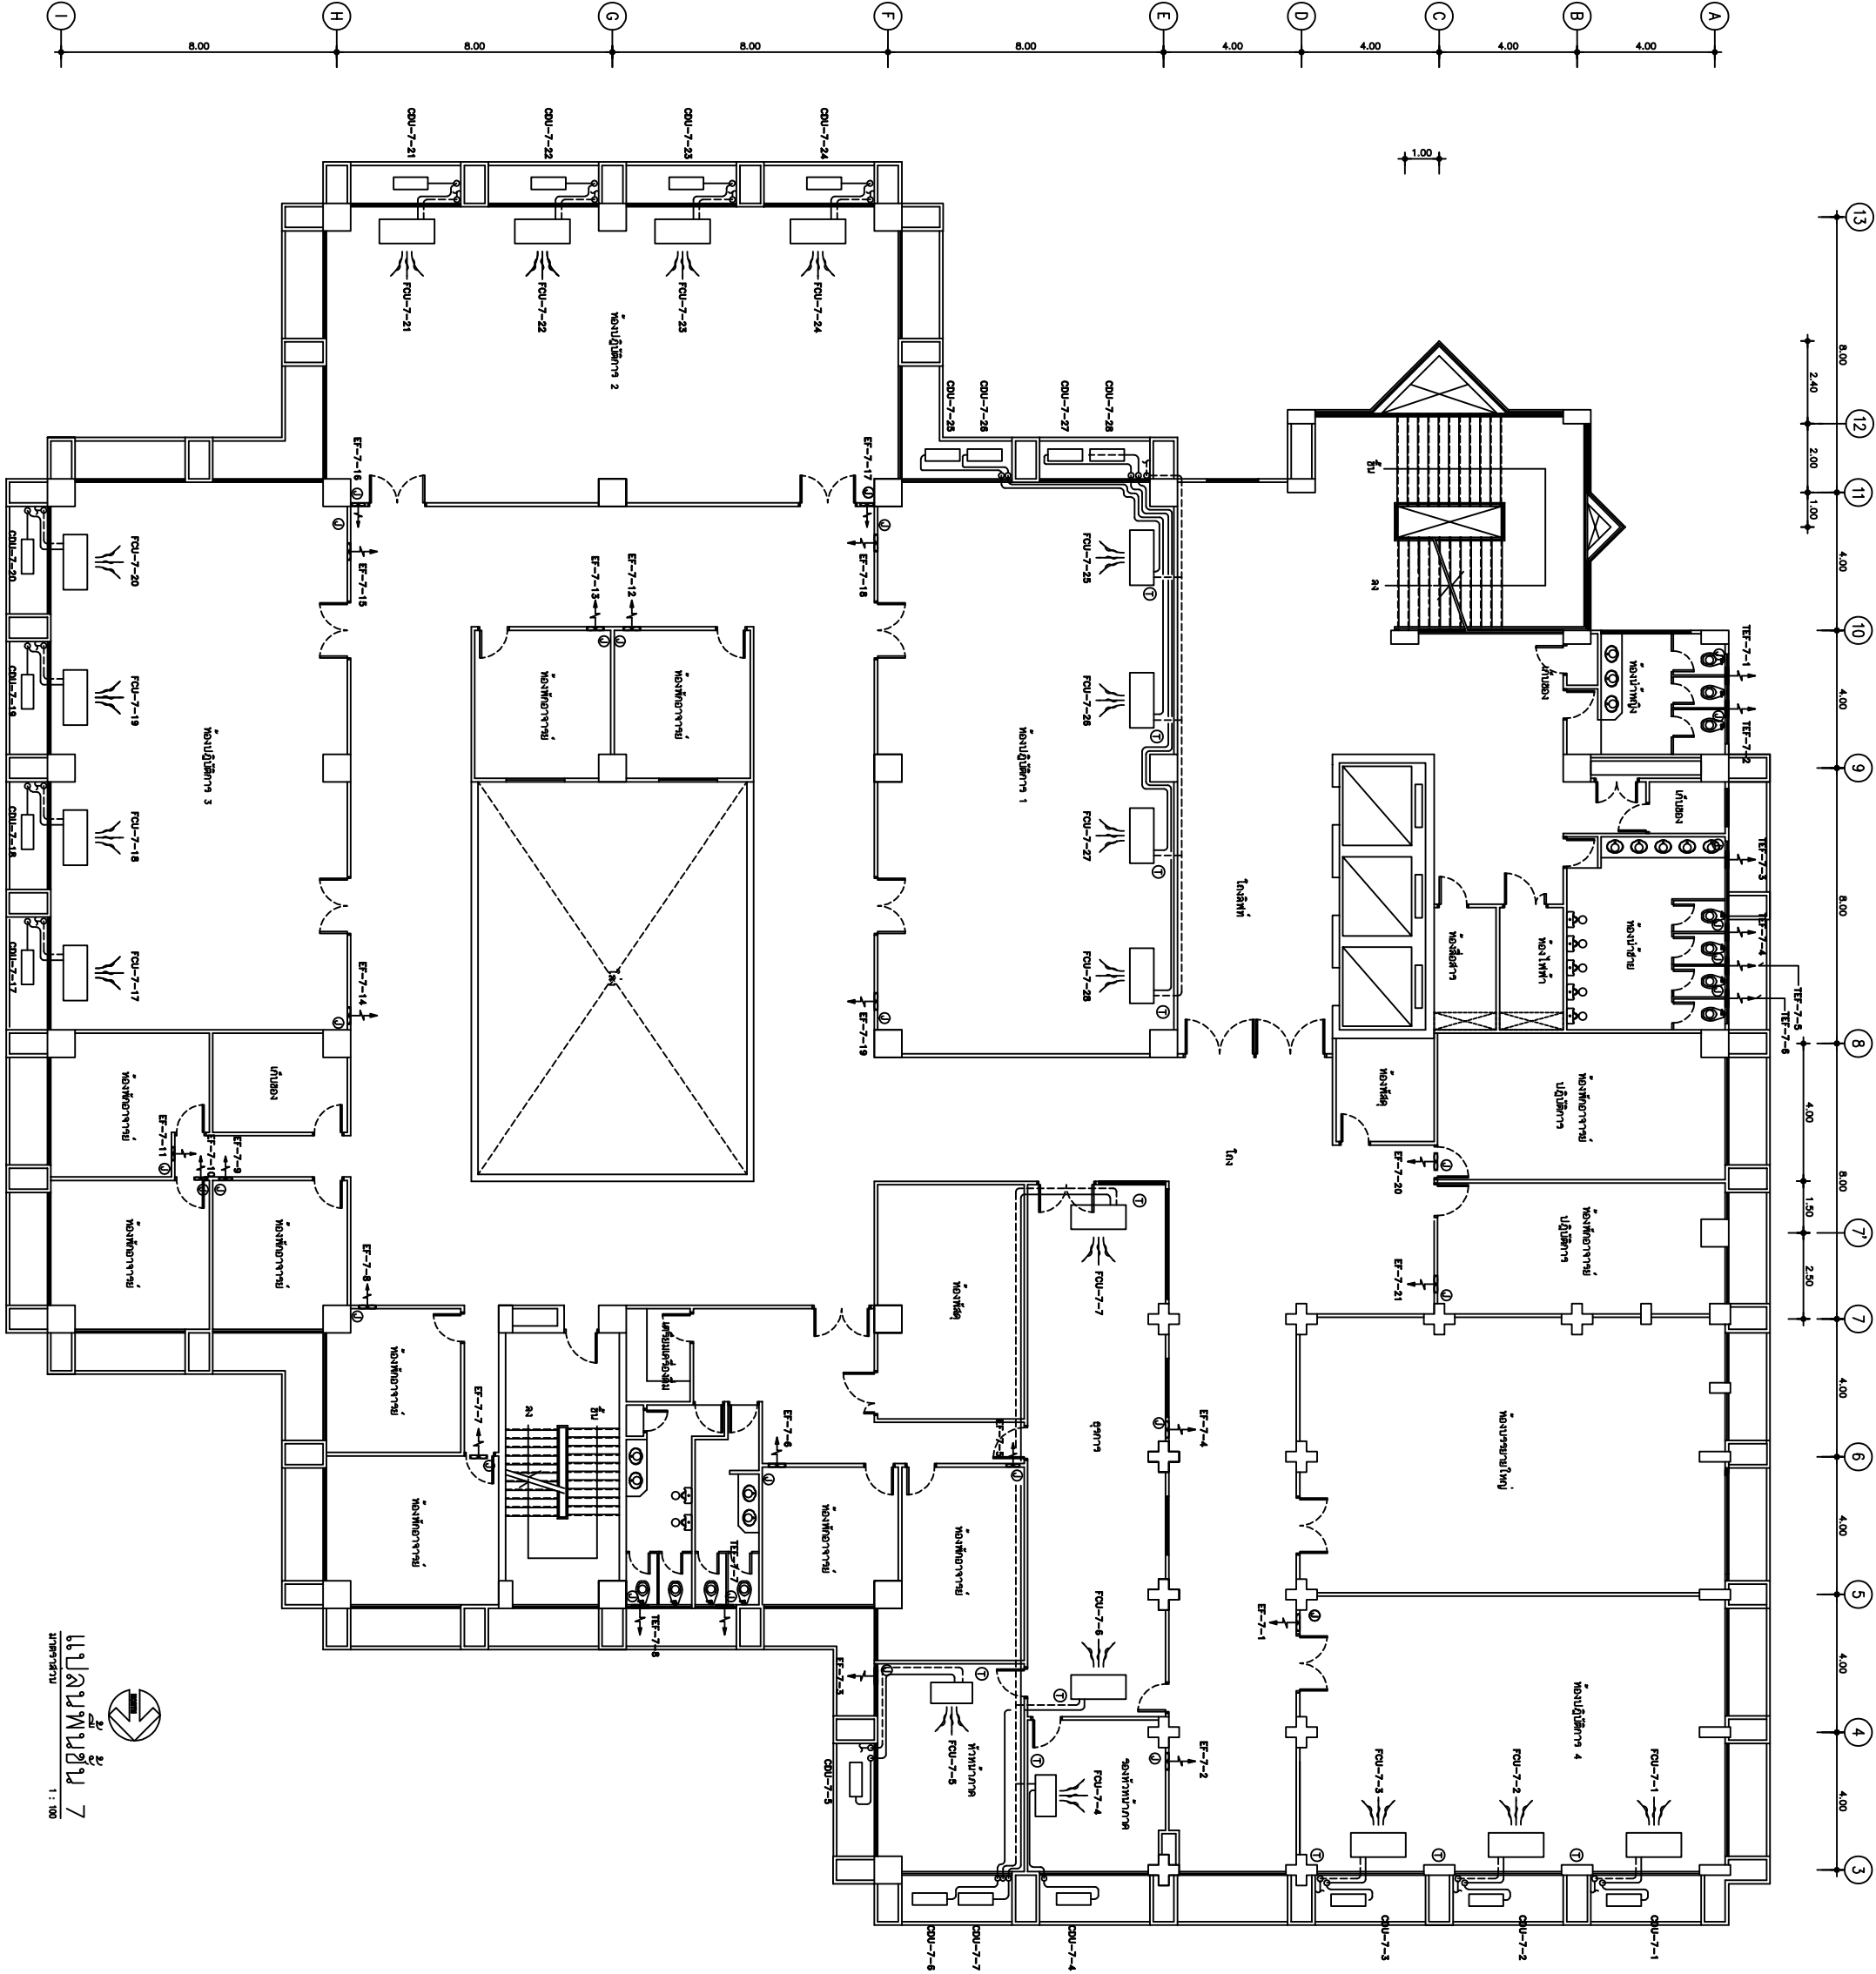

แปลนพื้นชั้น 7
1 : 100