

บริษัท เจ-สัน คอนสตรัคชั่น (ประเทศไทย) จำกัด
J-SONS CONSTRUCTION (THAILAND) COMPANY LIMITED
193/36-37 ถนนพหลโยธิน แขวงจตุจักร เขตจตุจักร กรุงเทพฯ 10130
Tel. (053) 214963 Fax. (053) 219842

ASBULT DRAWING

อาคารเรียนและปฏิบัติการ
คณะวิศวกรรมศาสตร์
มหาวิทยาลัยเชียงใหม่

OWNER

คณะวิศวกรรมศาสตร์ มหาวิทยาลัยเชียงใหม่

ARCHITECTS

设计院 设计人 姓名 82 岁

STRUCTURAL ENGINEERS

设计院 设计人 姓名 16450

SANITARY ENGINEERS

设计院 设计人 姓名 18024

ELECTRICAL ENGINEERS

设计院 设计人 姓名 828
设计院 设计人 姓名 20108

MECHANICAL ENGINEERS

设计院 设计人 姓名 8137

DRAWN

设计院 设计人

SHEET TITLE

LIGHTING SYSTEM LAYOUT
ON 5TH FLOOR (CEILING PLAN)

SCALE : AS SHOWN


DATE : 3 พฤษภาคม 2542

APPROVED :

DATE :

DRAWING NO. TOTAL SHEET

EE-26 46

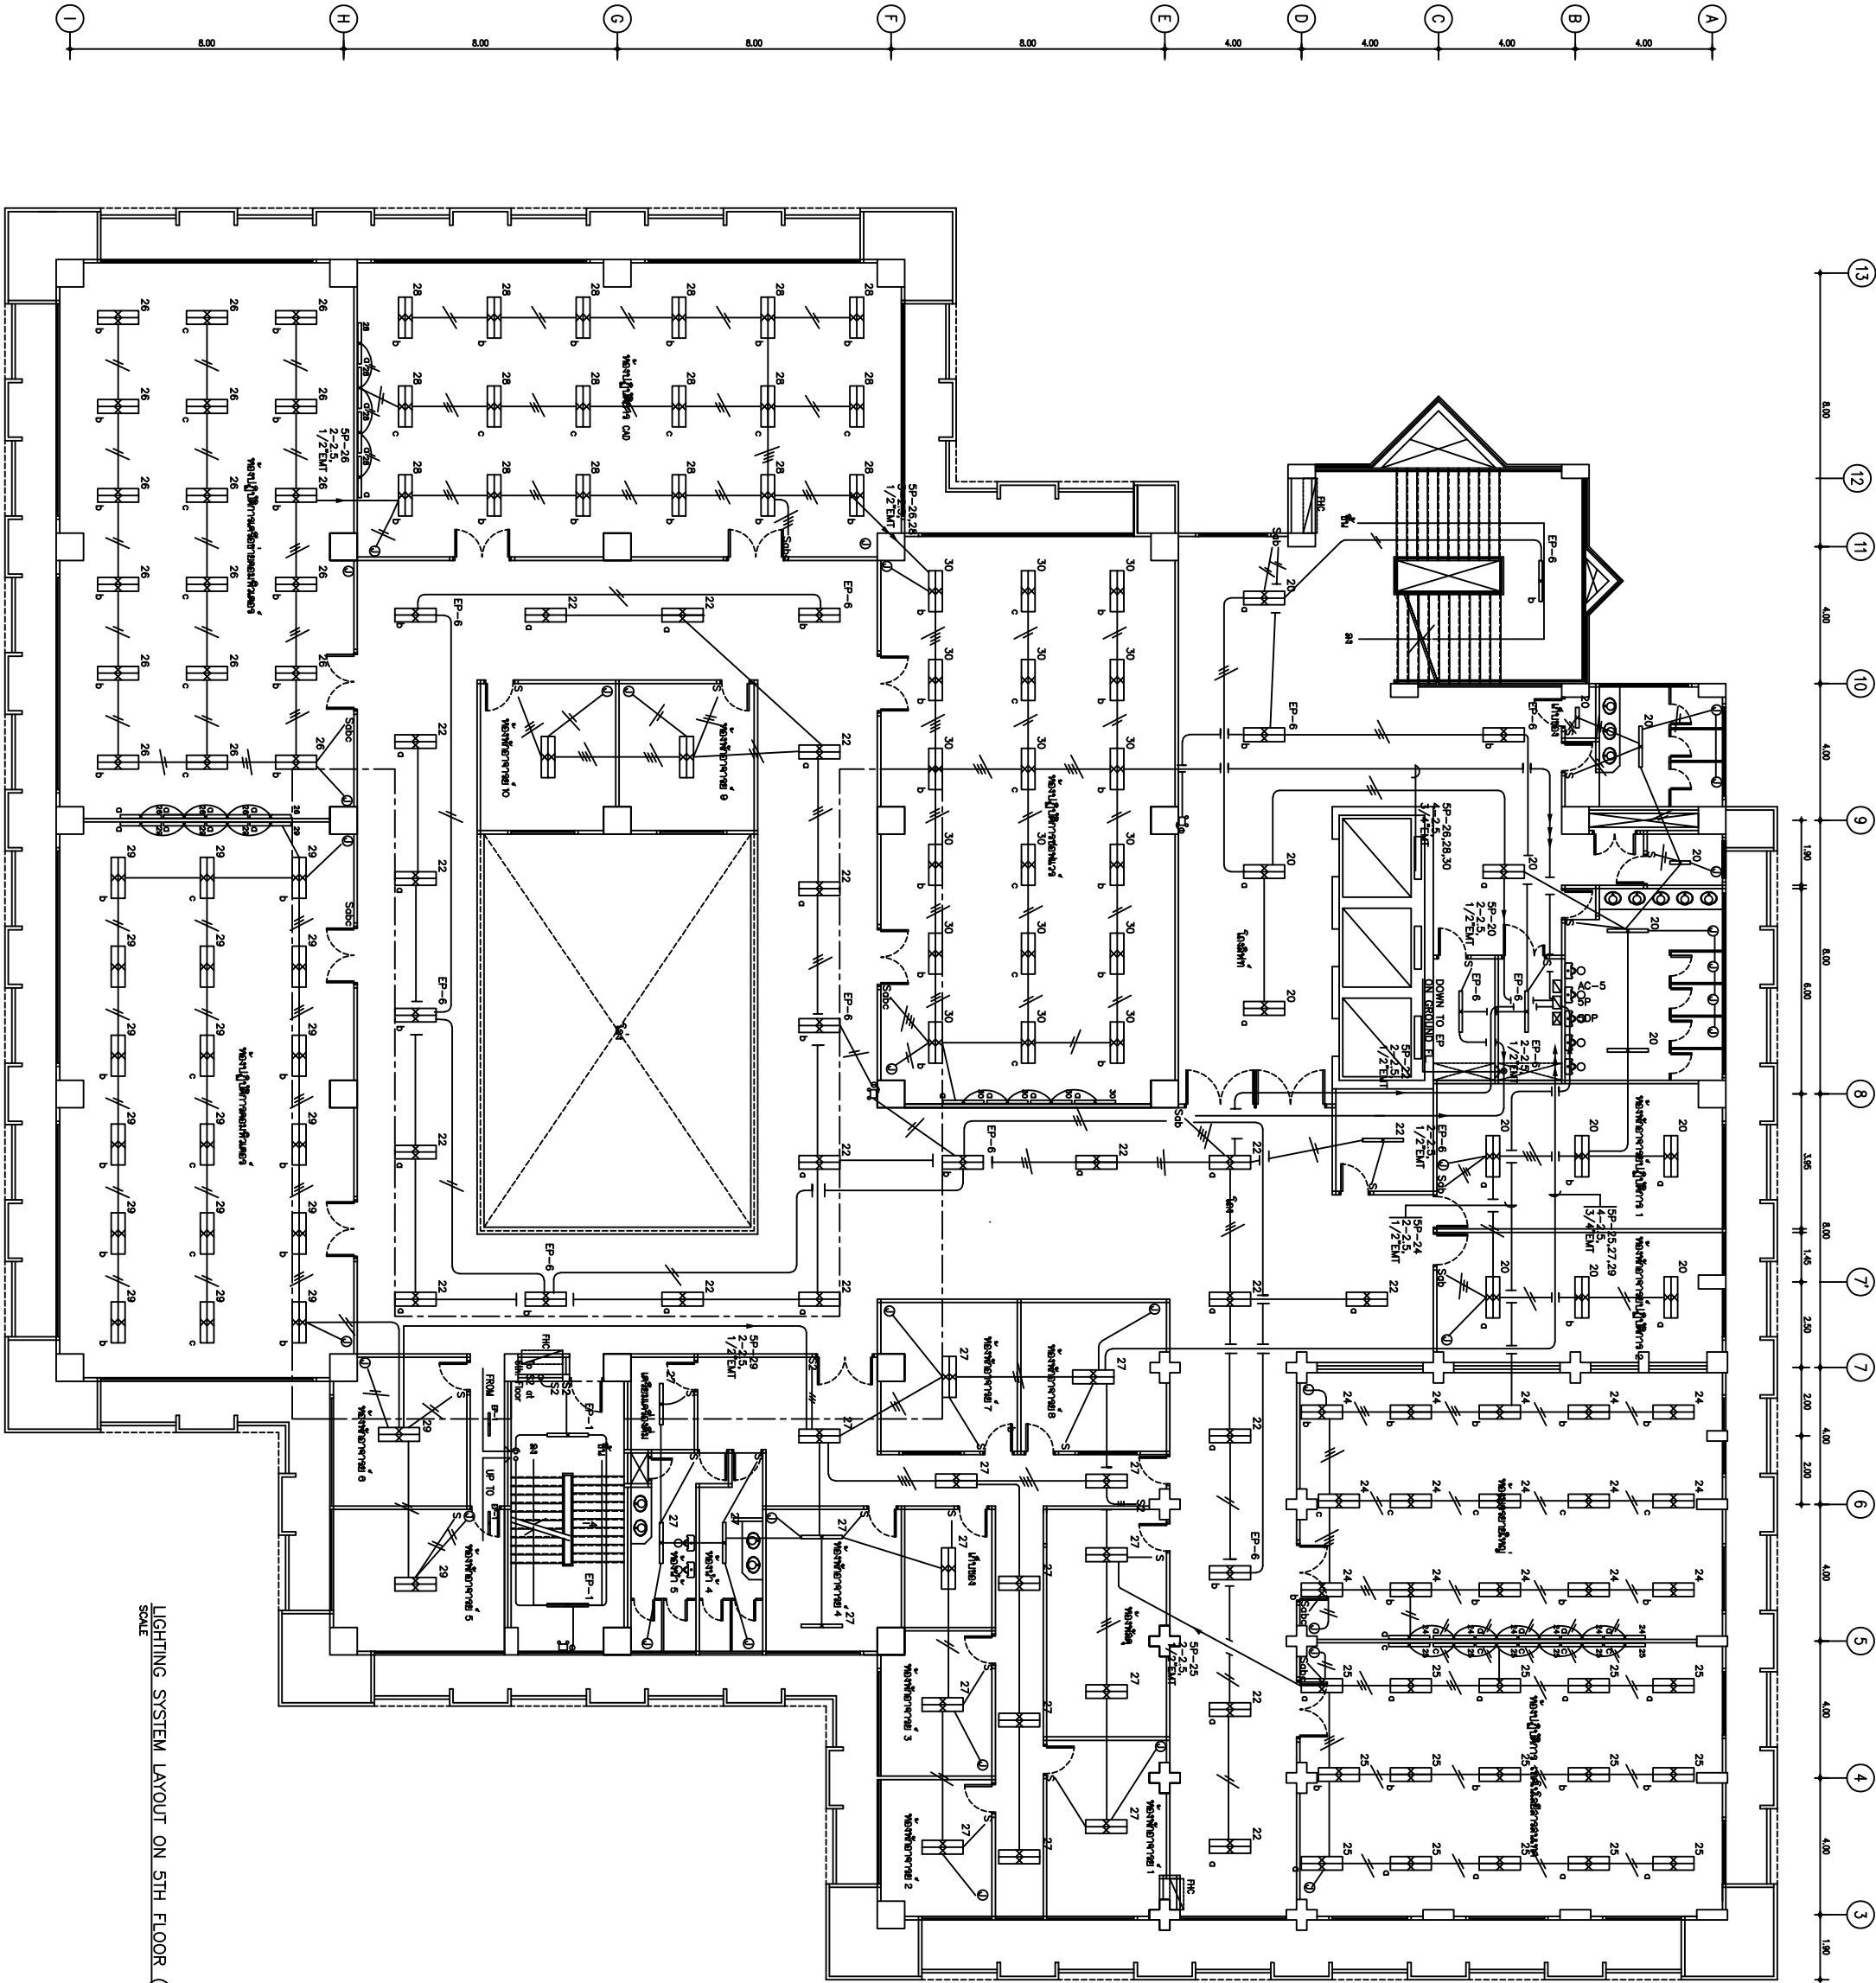

LIGHTING SYSTEM LAYOUT ON 5TH FLOOR (CEILING PLAN)
SCALE 1:100