

บริษัท เอ-สัน คอนสตรัคชั่น (ประเทศไทย) จำกัด
J-SONS CONSTRUCTION (THAILAND) COMPANY LIMITED
193/26-37 ถนนพหลโยธิน แขวงจตุจักร เขตจตุจักร กรุงเทพฯ 10130
Tel. (053) 214963 Fax. (053) 219842

ASBULT DRAWING

สถาปนิก วิศวกร และ สถาปนิก
ออกแบบอาคารและโครงสร้าง
อาคารจากแบบแปลน

OWNER

คณะผู้บริหารและผู้บริหาร

ARCHITECTS

บริษัท สถาปนิก วิศวกร 22 ส

STRUCTURAL ENGINEERS

บริษัท สถาปนิก วิศวกร 16450

SANITARY ENGINEERS

บริษัท สถาปนิก วิศวกร 18024

ELECTRICAL ENGINEERS

บริษัท สถาปนิก วิศวกร 828
กรุงเทพฯ 20108

MECHANICAL ENGINEERS

บริษัท สถาปนิก วิศวกร 8137

DRAWN

บริษัท สถาปนิก

SHEET TITLE

LIGHTING SYSTEM

LAYOUT ON 8TH FLOOR (CEILING PLAN)

SCALE : AS SHOWN


DATE : 5 พฤษภาคม 2542

APPROVED :

DATE :

DRAWING NO. TOTAL SHEET

EE-40 46

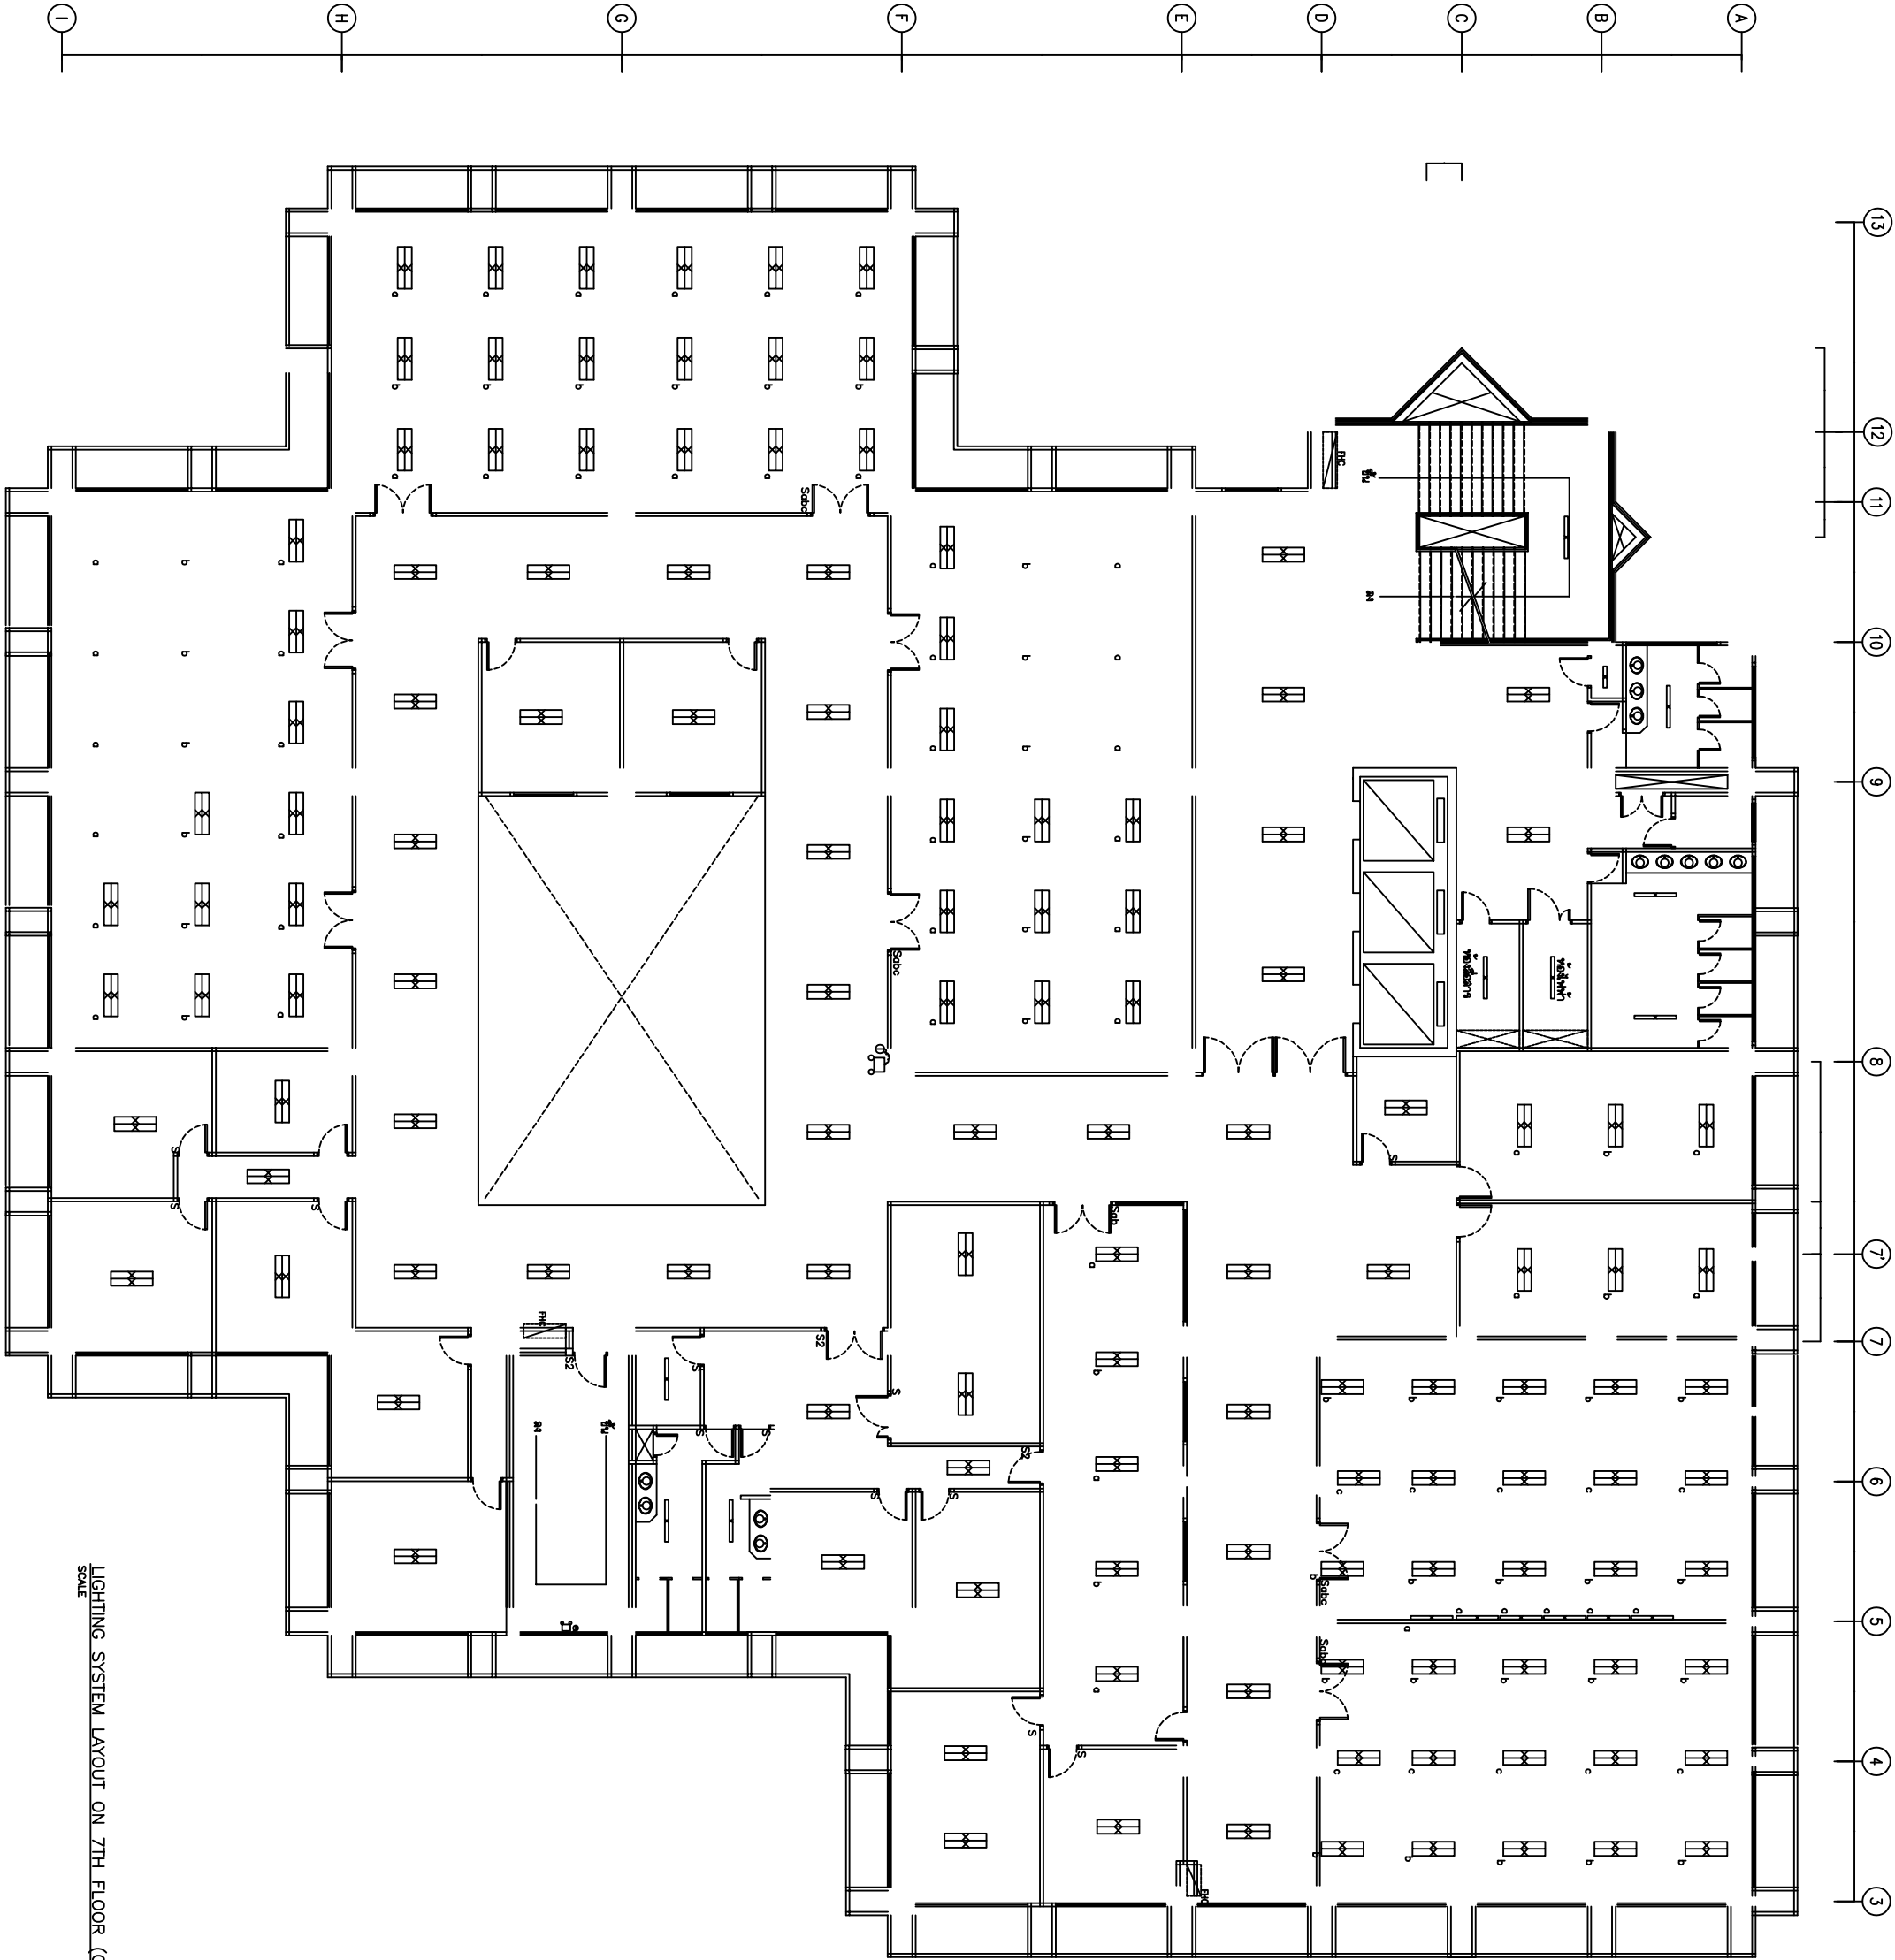

LIGHTING SYSTEM LAYOUT ON 7TH FLOOR (CEILING PLAN)
SCALE 1:100