

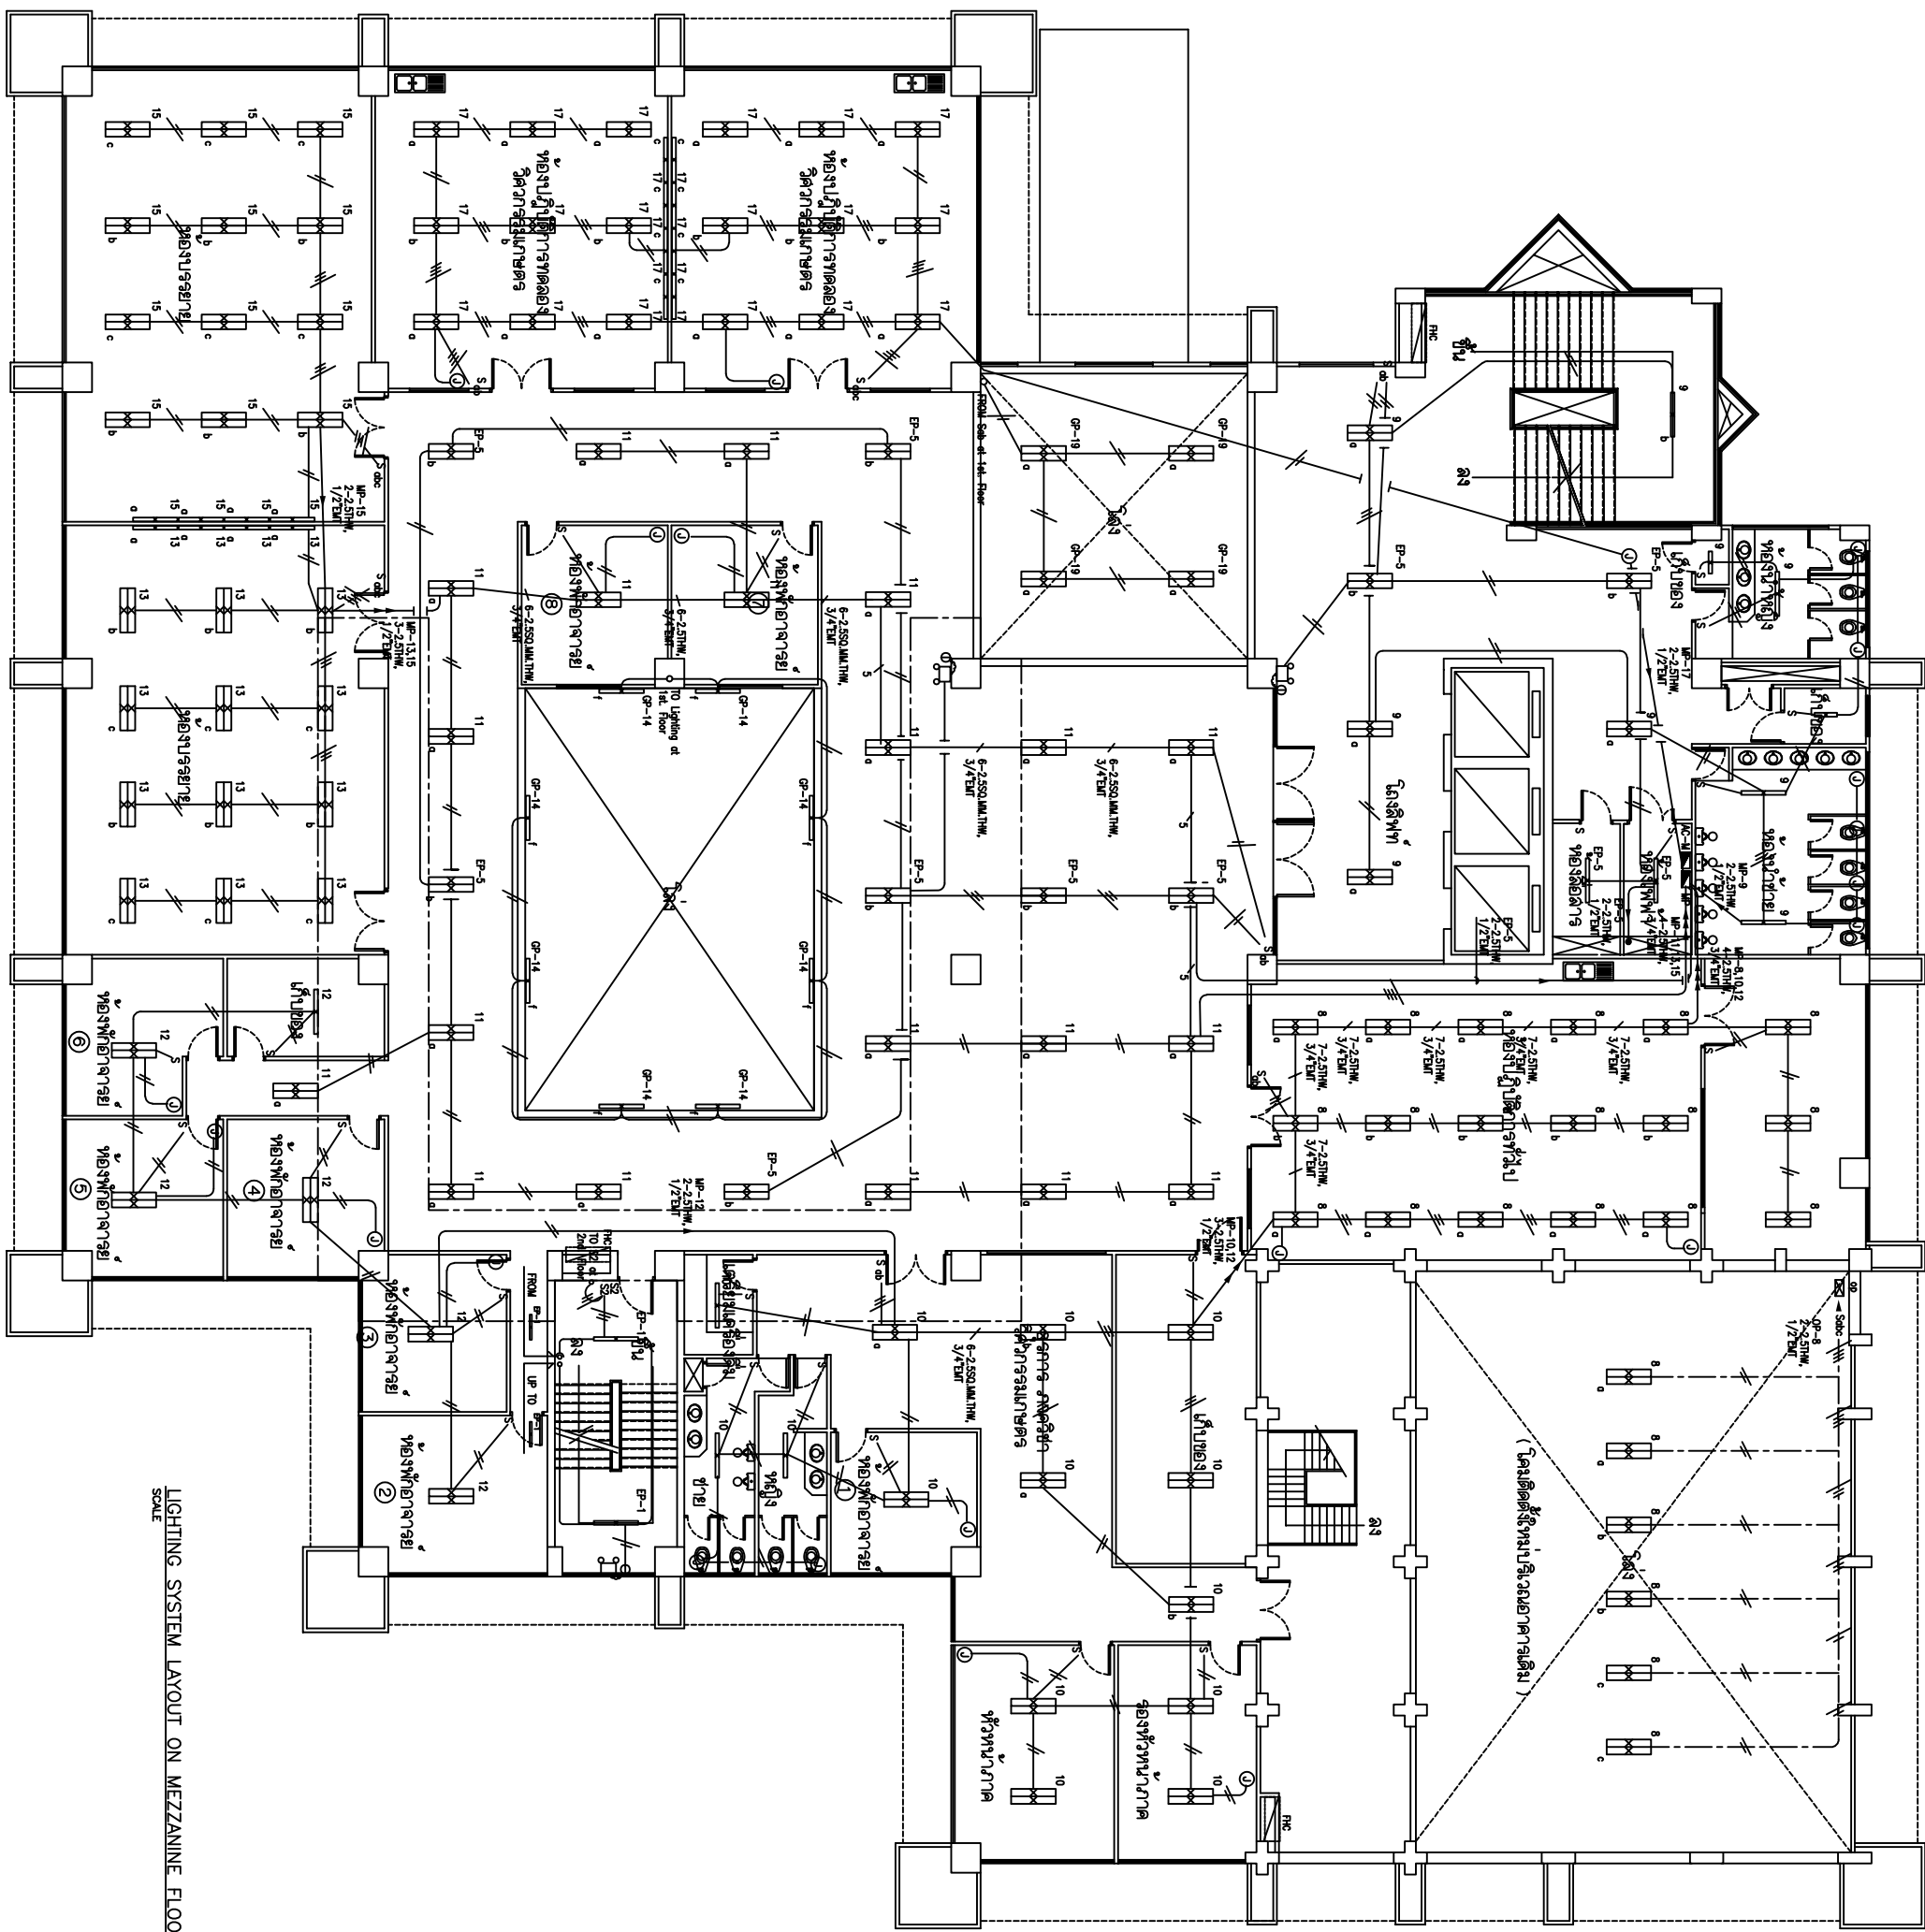
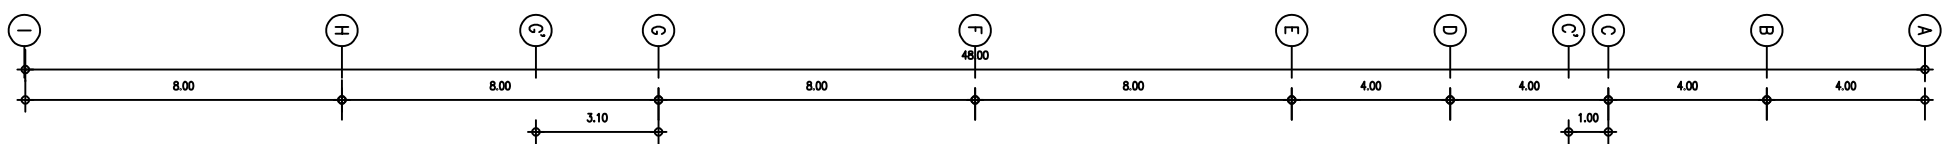


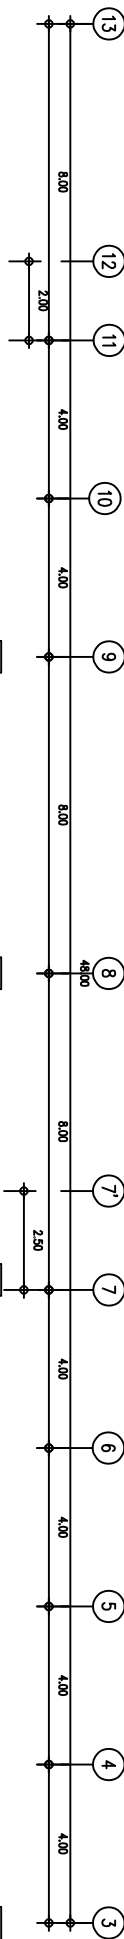

LIGHTING SYSTEM LAYOUT ON MEZZANINE FLOOR (FLOOR PLAN)
SCALE 1:100

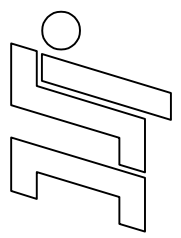

บริษัท เจ-สัน คอนสตรัคชั่น (ประเทศไทย) จำกัด
J-SONS CONSTRUCTION (THAILAND) COMPANY LIMITED
893/36-37 ถนนพหลโยธิน แขวงจตุจักร เขตจตุจักร กรุงเทพฯ 10130
Tel. (053) 214963 Fax. (053) 219842

ASBULT DRAWING

สถาปนิกชั้นบนและบันไดขึ้นอาคาร
คณะวิศวกรของบริษัท
มหาวิทยาลัยเทคโนโลยีพระจอมเกล้าธนบุรี

OWNER
คณะวิศวกรรมศาสตร์ มหาวิทยาลัยเทคโนโลยีพระจอมเกล้าธนบุรี

ARCHITECTS
เชื้อน ธีรพัฒน์ งาม 82 2

STRUCTURAL ENGINEERS
เชื้อน ธีรพัฒน์ งาม 16450

SANITARY ENGINEERS
เชื้อน ธีรพัฒน์ งาม 18024

ELECTRICAL ENGINEERS
เชื้อน ธีรพัฒน์ งาม 828
เกษม ธีรพัฒน์ งาม 20108

MECHANICAL ENGINEERS
เชื้อน ธีรพัฒน์ งาม 8137

DRAWN
เชื้อน ธีรพัฒน์ งาม

SHEET TITLE
LIGHTING SYSTEM LAYOUT
ON MEZZANINE FLOOR (FLOOR PLAN)

SCALE : AS SHOWN
DATE : 3 พฤษภาคม 2542

APPROVED :
DATE :

DRAWING NO. TOTAL SHEET

EE-11 46