



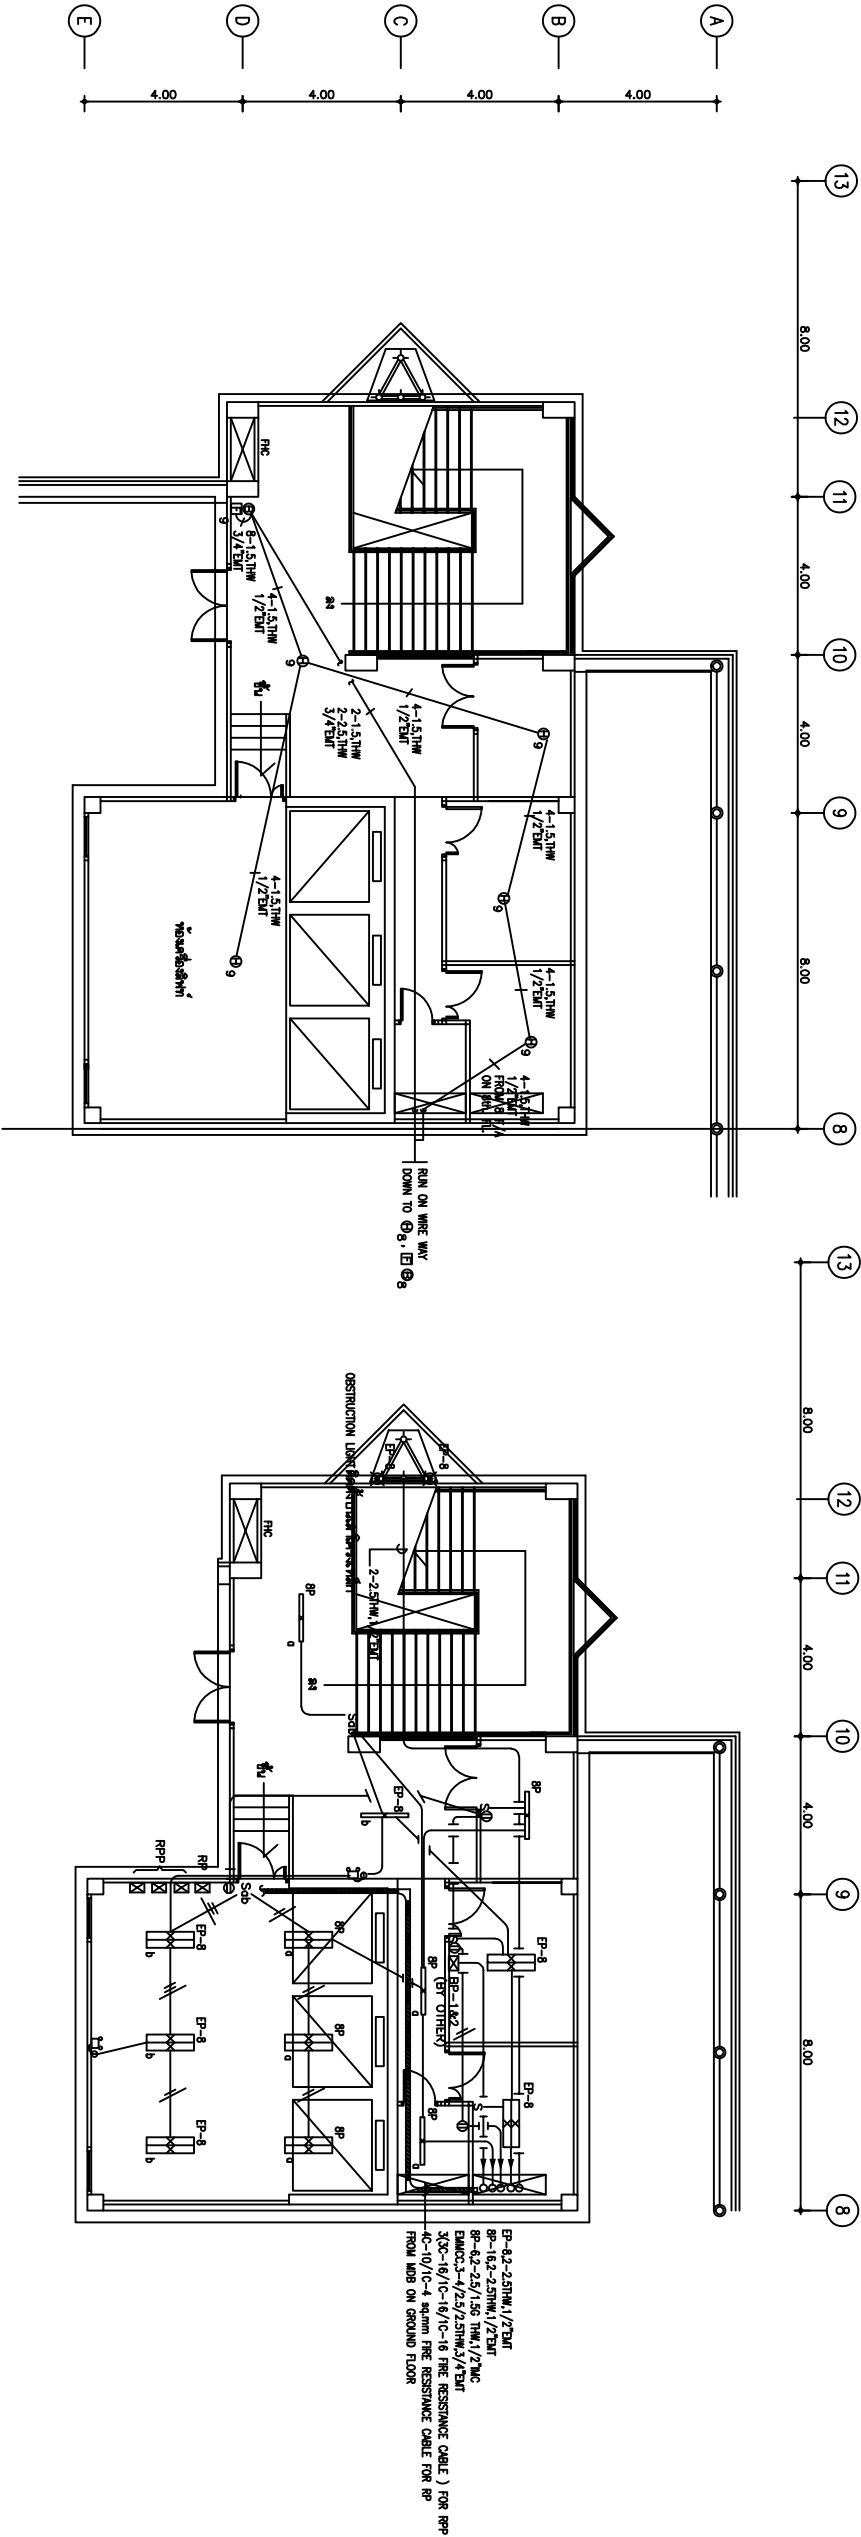

FIRE ALARM SYSTEM LAYOUT ON ROOF FLOOR (FLOOR&CEILING PLAN)

SCALE


1:100

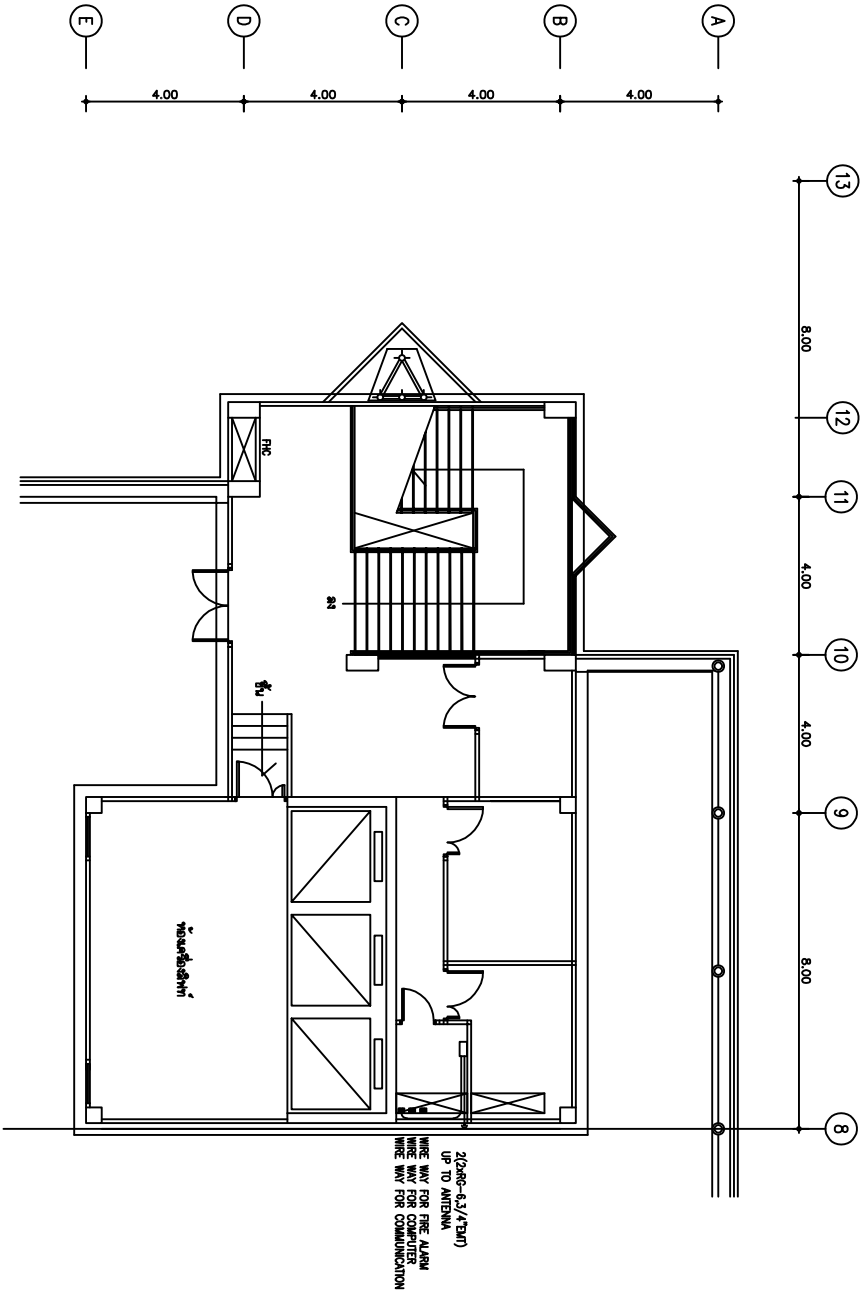

FIRE ALARM SYSTEM LAYOUT ON ROOF FLOOR (FLOOR&CEILING PLAN)

SCALE


1:100

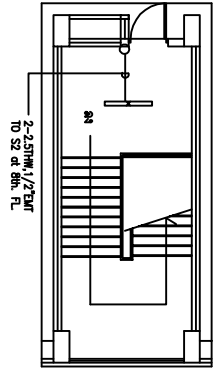

ELECTRICAL SYSTEM LAYOUT ON ROOF FLOOR (FLOOR&CEILING PLAN)

SCALE

1:100

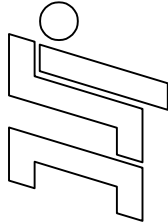

บริษัท เจ-สัน คอนสตรัคชั่น (ประเทศไทย) จำกัด
J-SONS CONSTRUCTION (THAILAND) COMPANY LIMITED
83/36-37 ถนนวิภาวดีรังสิต แขวงจตุจักร กรุงเทพฯ 10310
Tel. (053) 214963 Fax. (053) 219842

ASBULT DRAWING

สถาปัตย์วิศวกรรมและภูมิสถาปัตย์
คณะวิศวกรรมศาสตร์
มหาวิทยาลัยเทคโนโลยีพระจอมเกล้าธนบุรี

OWNER

คณะวิศวกรรมศาสตร์ มหาวิทยาลัยเทคโนโลยีพระจอมเกล้าธนบุรี

ARCHITECTS

แผ่นม อธิพานนท์ ส. 62 ส

STRUCTURAL ENGINEERS

บุญชัย พันธ์พานิชกุล ฐ. 16450

SANITARY ENGINEERS

จ.ล.พ.ล. ส.วิภาวดีรังสิต ฐ. 18024

ELECTRICAL ENGINEERS

เอกภพ อภิธรรมรัตน์ ส.ท. 828
กฤษณะ อธิพานิชกุล ฐ. 20108

MECHANICAL ENGINEERS

สมศักดิ์ อธิพานิชกุล ฐ. 8137

DRAWN

วิภาวดี อธิพานิชกุล

SHEET TITLE

FIRE ALARM SYSTEM LAYOUT ON ROOF FLOOR
(FLOOR&CEILING PLAN)
WAV SYSTEM LAYOUT ON ROOF FLOOR
(FLOOR&CEILING PLAN)
ELECTRICAL SYSTEM LAYOUT ON ROOF FLOOR
(FLOOR&CEILING PLAN)

SCALE : AS SHOWN

DATE : 28 มกราคม 2542

APPROVED :

DATE :

DRAWING NO. TOTAL SHEET

EE-45 46