

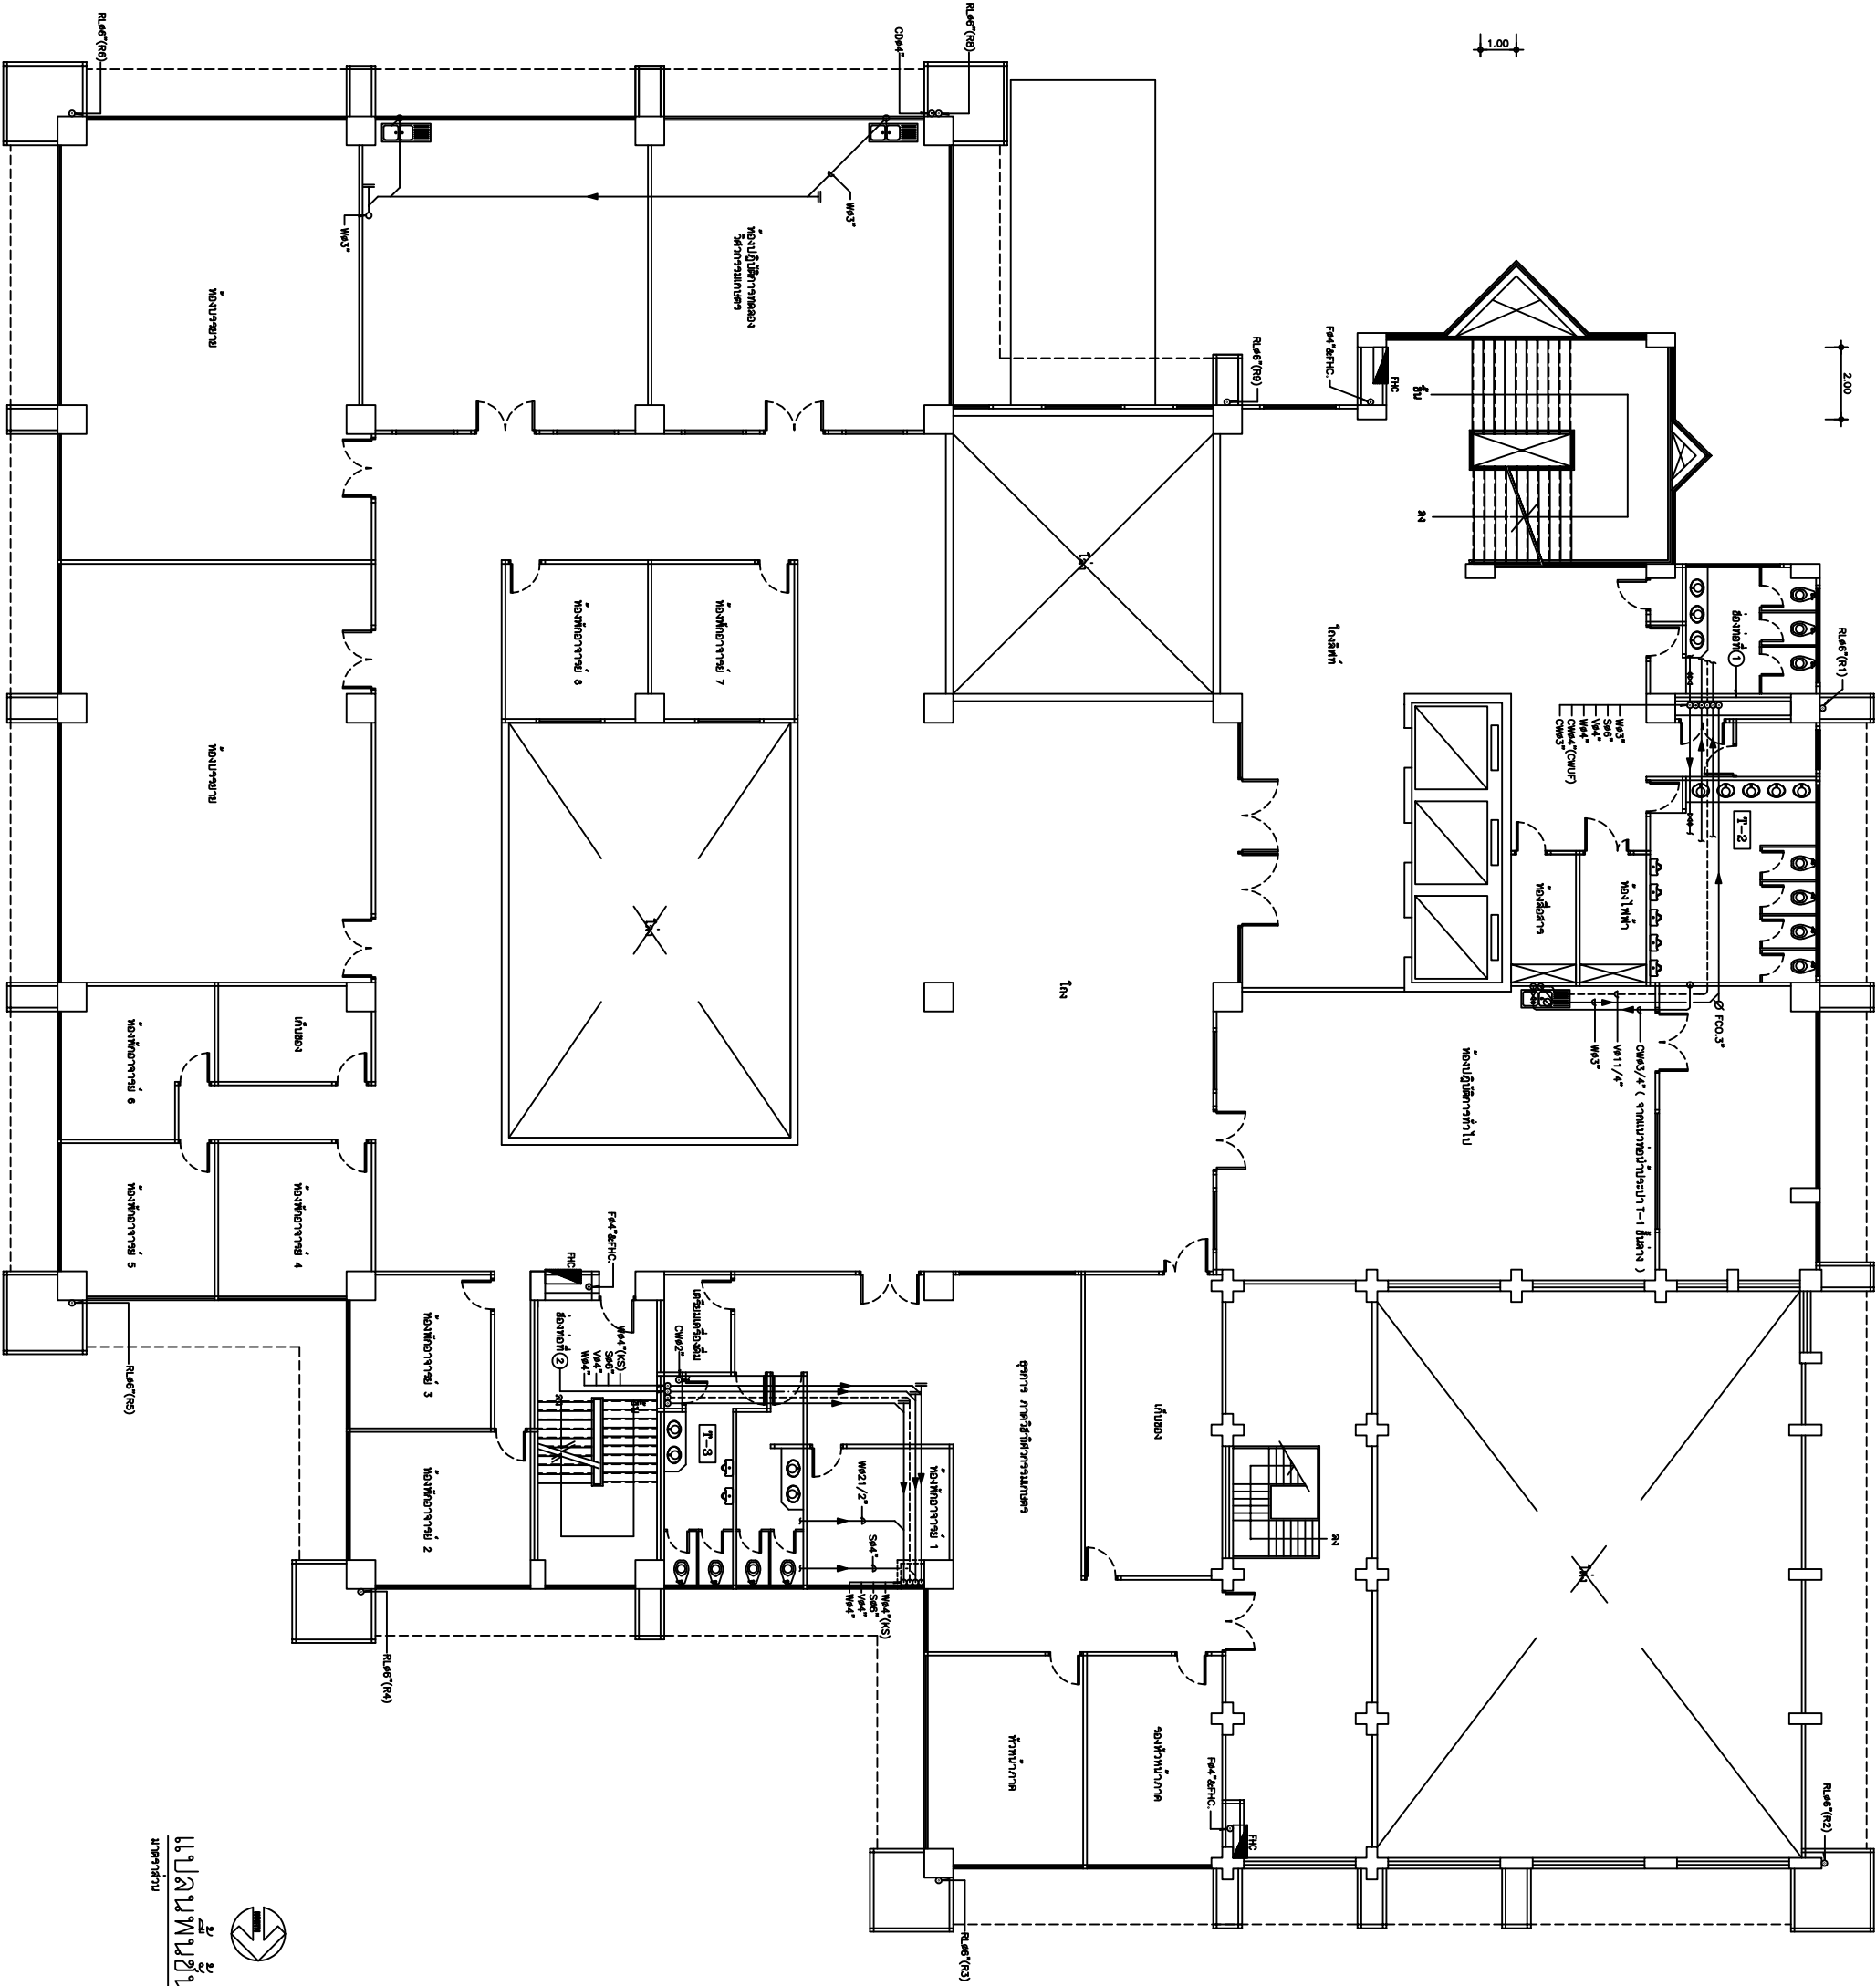
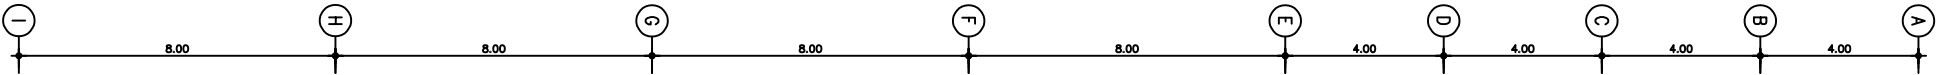


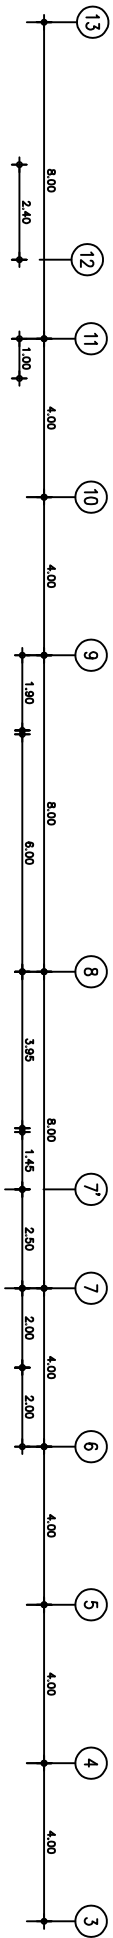

แปลนพื้นที่
1 : 100

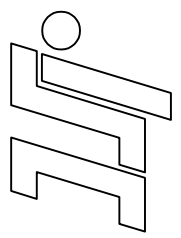

บริษัท เจ-สัน คอนสตรัคชั่น (ประเทศไทย) จำกัด
J-SONS CONSTRUCTION (THAILAND) COMPANY LIMITED
193/36-37 ถนนพหลโยธิน แขวงจตุจักร กรุงเทพฯ 10130
Tel. (053) 214963 Fax. (053) 219842

ASBULT DRAWING

สถาปนิกชั้นบนและบันได
คณะวิศวกรของสถาปัตย์
มหาวิทยาลัยศิลปากร

OWNER

คณะวิศวกรรมศาสตร์ มหาวิทยาลัยเชียงใหม่

ARCHITECTS

เขียน ธีรพัฒน์ งาม 82 ส

STRUCTURAL ENGINEERS

เขียน ธีรพัฒน์ งาม 82 ส

SANITARY ENGINEERS

เขียน ธีรพัฒน์ งาม 82 ส

ELECTRICAL ENGINEERS

เอก ธีรพัฒน์ งาม 82 ส
กษณะ ธีรพัฒน์ งาม 20108

MECHANICAL ENGINEERS

เอก ธีรพัฒน์ งาม 82 ส

DRAWN

เขียน ธีรพัฒน์ งาม 82 ส

SHEET TITLE

แบบแปลนพื้นที่

SCALE : 1 : 100

DATE : 1 สิงหาคม 2542

APPROVED :

DATE :

DRAWING NO. TOTAL SHEET

SN-04 26