

บริษัท เอ-สัน คอนสตรัคชั่น (ประเทศไทย) จำกัด
J-SONS CONSTRUCTION (THAILAND) COMPANY LIMITED
193/26-37 ถนนพหลโยธิน แขวงจตุจักร เขตจตุจักร กรุงเทพฯ 10130
Tel. (053) 214963 Fax. (053) 219842

ASBULT DRAWING

สถาปนิกชั้นบนและบันไดขึ้นอาคาร
คณะวิศวกรของบริษัท
มหาวิทยาลัยเทคโนโลยีพระจอมเกล้าธนบุรี

OWNER

คณะวิศวกรรมศาสตร์ มหาวิทยาลัยเทคโนโลยีพระจอมเกล้าธนบุรี

ARCHITECTS

เขียน ธีรพัฒน์ งาม 82 ส

STRUCTURAL ENGINEERS

เขียน ธีรพัฒน์ งาม 16450

SANITARY ENGINEERS

เขียน ธีรพัฒน์ งาม 17665

ELECTRICAL ENGINEERS

เอกา ธีรพัฒน์ งาม 828
เกษม ธีรพัฒน์ งาม 20108

MECHANICAL ENGINEERS

เอกา ธีรพัฒน์ งาม 8137

DRAWN

เขียน ธีรพัฒน์ งาม

SHEET TITLE

แบบแปลนชั้น 2-3

SCALE : 1 : 100


DATE : 1 สิงหาคม 2542

APPROVED :

DATE :

DRAWING NO. TOTAL SHEET

SN-05 26

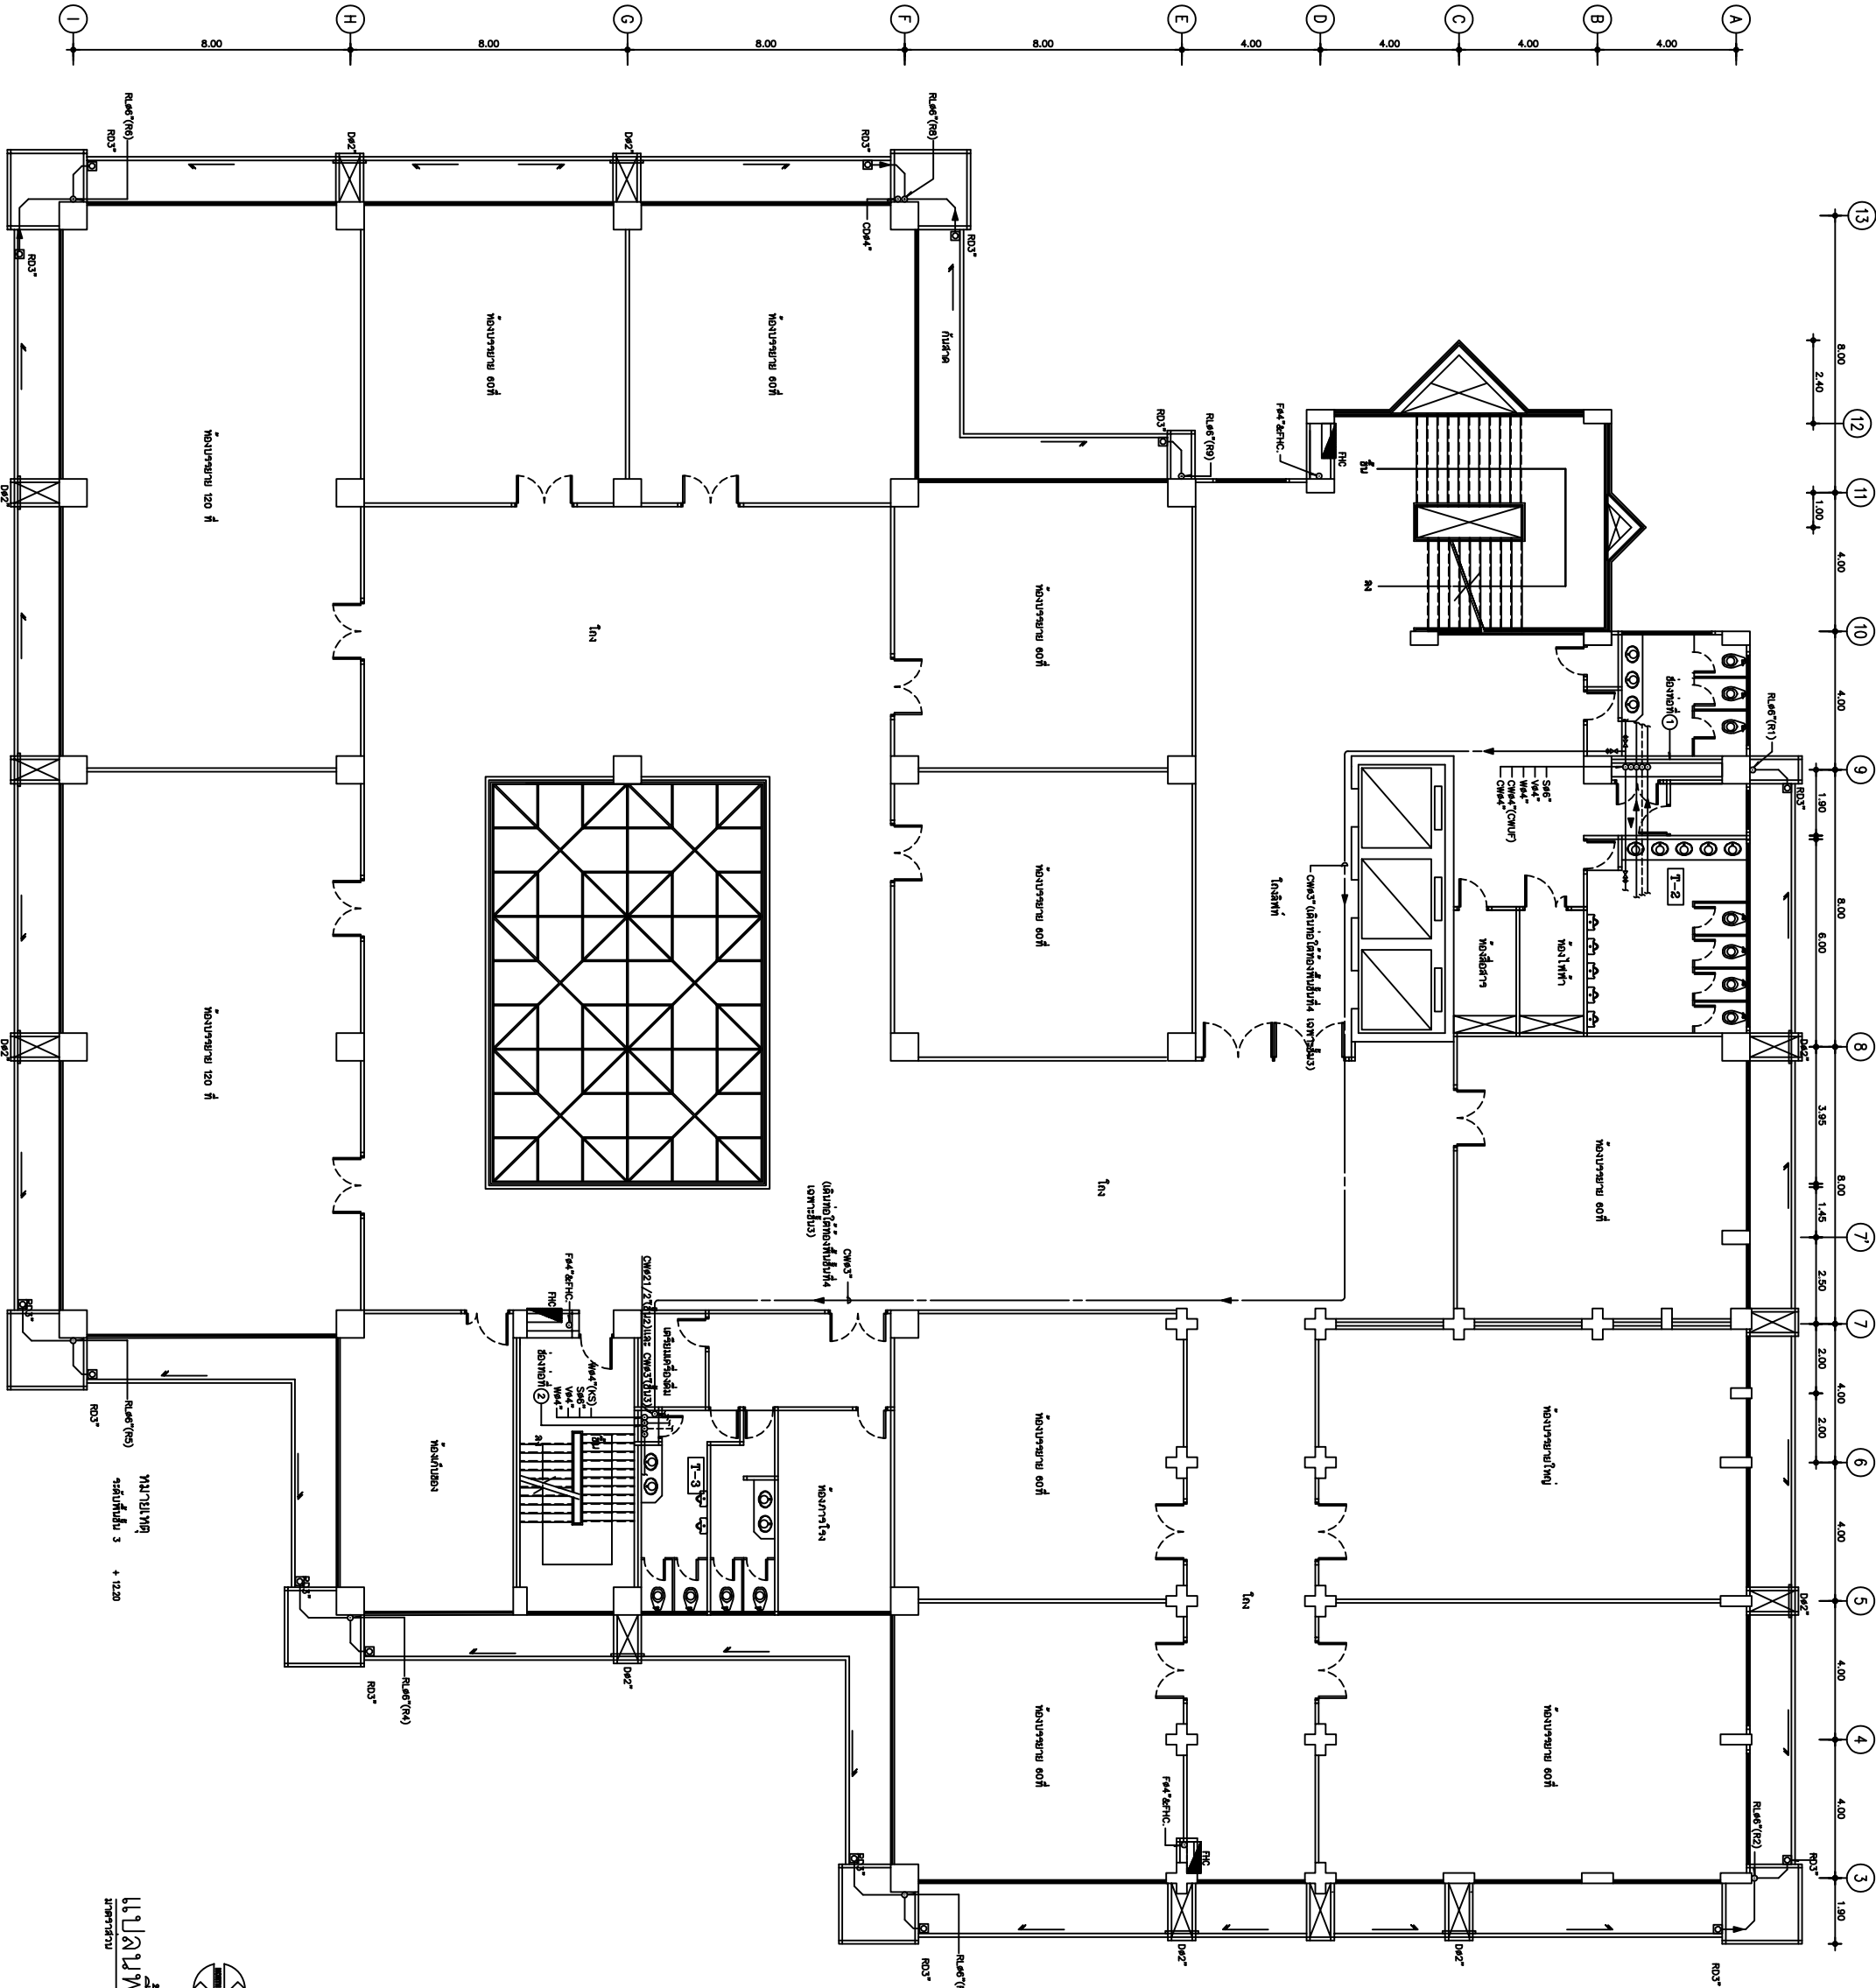

แบบแปลนชั้น 2-3
1 : 100