

บริษัท เอ-สัน คอนสตรัคชั่น (ประเทศไทย) จำกัด
J-SONS CONSTRUCTION (THAILAND) COMPANY LIMITED
193/26-37 ถนนพหลโยธิน แขวงจตุจักร เขตจตุจักร กรุงเทพฯ 10130
Tel. (053) 214963 Fax. (053) 219842

ASBULT DRAWING

สถาปนารังสรรค์และปฏิบัติงานการ
ออกแบบวิศวกรรมการก่อสร้าง
นิตยสารวิศวกรรมโยธา

OWNER

คณะกรรมการอำนวยการ มหาวิทยาลัยเชียงใหม่

ARCHITECTS

เขียน ธีรพัฒน์ งาม 82 ส

STRUCTURAL ENGINEERS

เจษฎ์ ทรัพย์วิวัฒน์ งาม 16450

SANITARY ENGINEERS

วิริยะ อำนวยวิทย์ งาม 17165

ELECTRICAL ENGINEERS

เอก ภัทริพงษ์ งาม 828
เกษม ธิณี งาม 20108

MECHANICAL ENGINEERS

ณัฏฐ์ อำนวยวิทย์ งาม 8137

DRAWN

วิริยะ อำนวย

SHEET TITLE

แบบแปลนอาคารที่พักอาศัย 7

SCALE : 1 : 100


DATE : 6 มิถุนายน 2542

APPROVED :

DATE :

DRAWING NO. TOTAL SHEET

SN-10 26

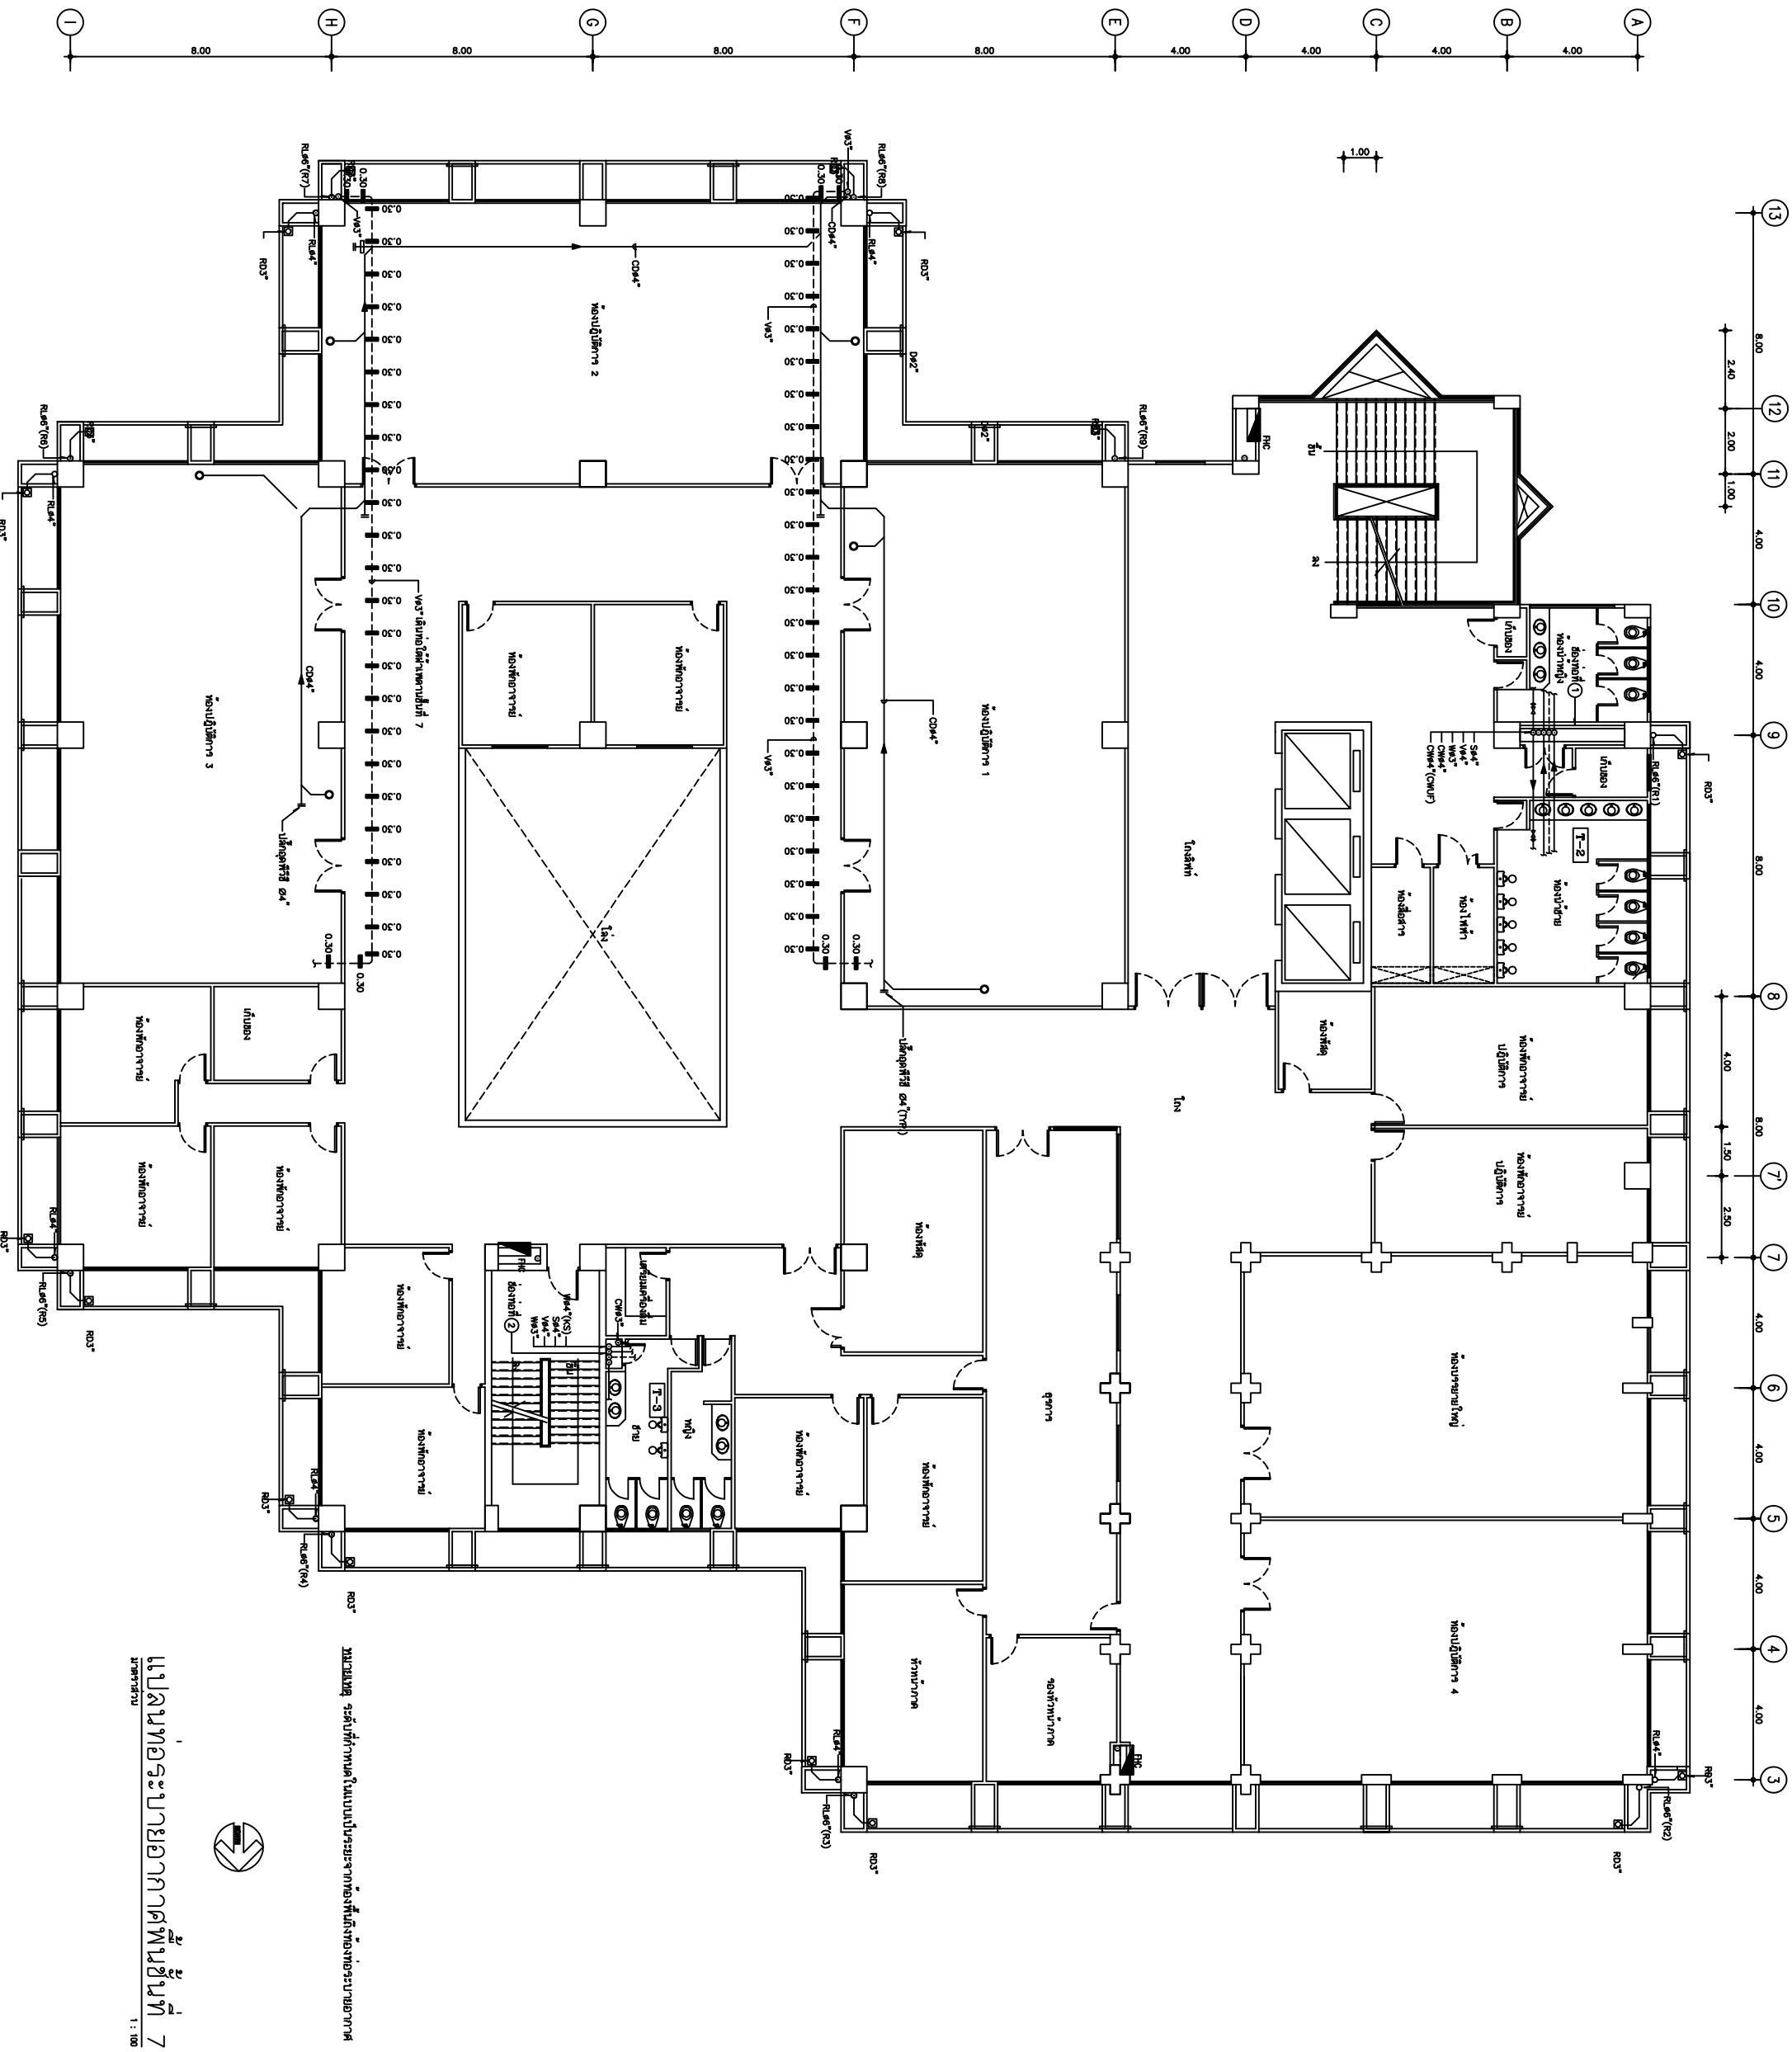

แปลนอาคารที่พักอาศัย 7
1 : 100