

บริษัท เอ-สัน คอนสตรัคชั่น (ประเทศไทย) จำกัด
J-SONS CONSTRUCTION (THAILAND) COMPANY LIMITED
193/26-37 ถนนพหลโยธิน แขวงจตุจักร เขตจตุจักร กรุงเทพฯ 10130
Tel. (053) 2149653 Fax. (053) 219842

ASBULT DRAWING

สถาปนาริเสนแบบและปฏิบัติงานการ
คำนวณราคาของอาคาร
นิตยาริสถาปนาริเขียนแบบ

OWNER

คณะบริหารมหาวิทยาลัย มหาวิทยาลัยเชียงใหม่

ARCHITECTS

เขียน ริชิตานนท์ จก. 82 ฉ

STRUCTURAL ENGINEERS

เชื้อย พริษฐ์วิธิน จก. 16450

SANITARY ENGINEERS

ริชิตย ริชิตานนท์ จก. 17165

ELECTRICAL ENGINEERS

เอกา ริชิตานนท์ จก. 828
เกษณะ ยินดี จก. 20108

MECHANICAL ENGINEERS

ฉนศิริ ฉันทะธา จก. 8137

DRAWN

ริชิตย ฉันทะ

SHEET TITLE

แบบแปลนชั้น 8

SCALE : 1 : 100


DATE : 8 มิถุนายน 2542

APPROVED :

DATE :

DRAWING NO. TOTAL SHEET

SN-12 26

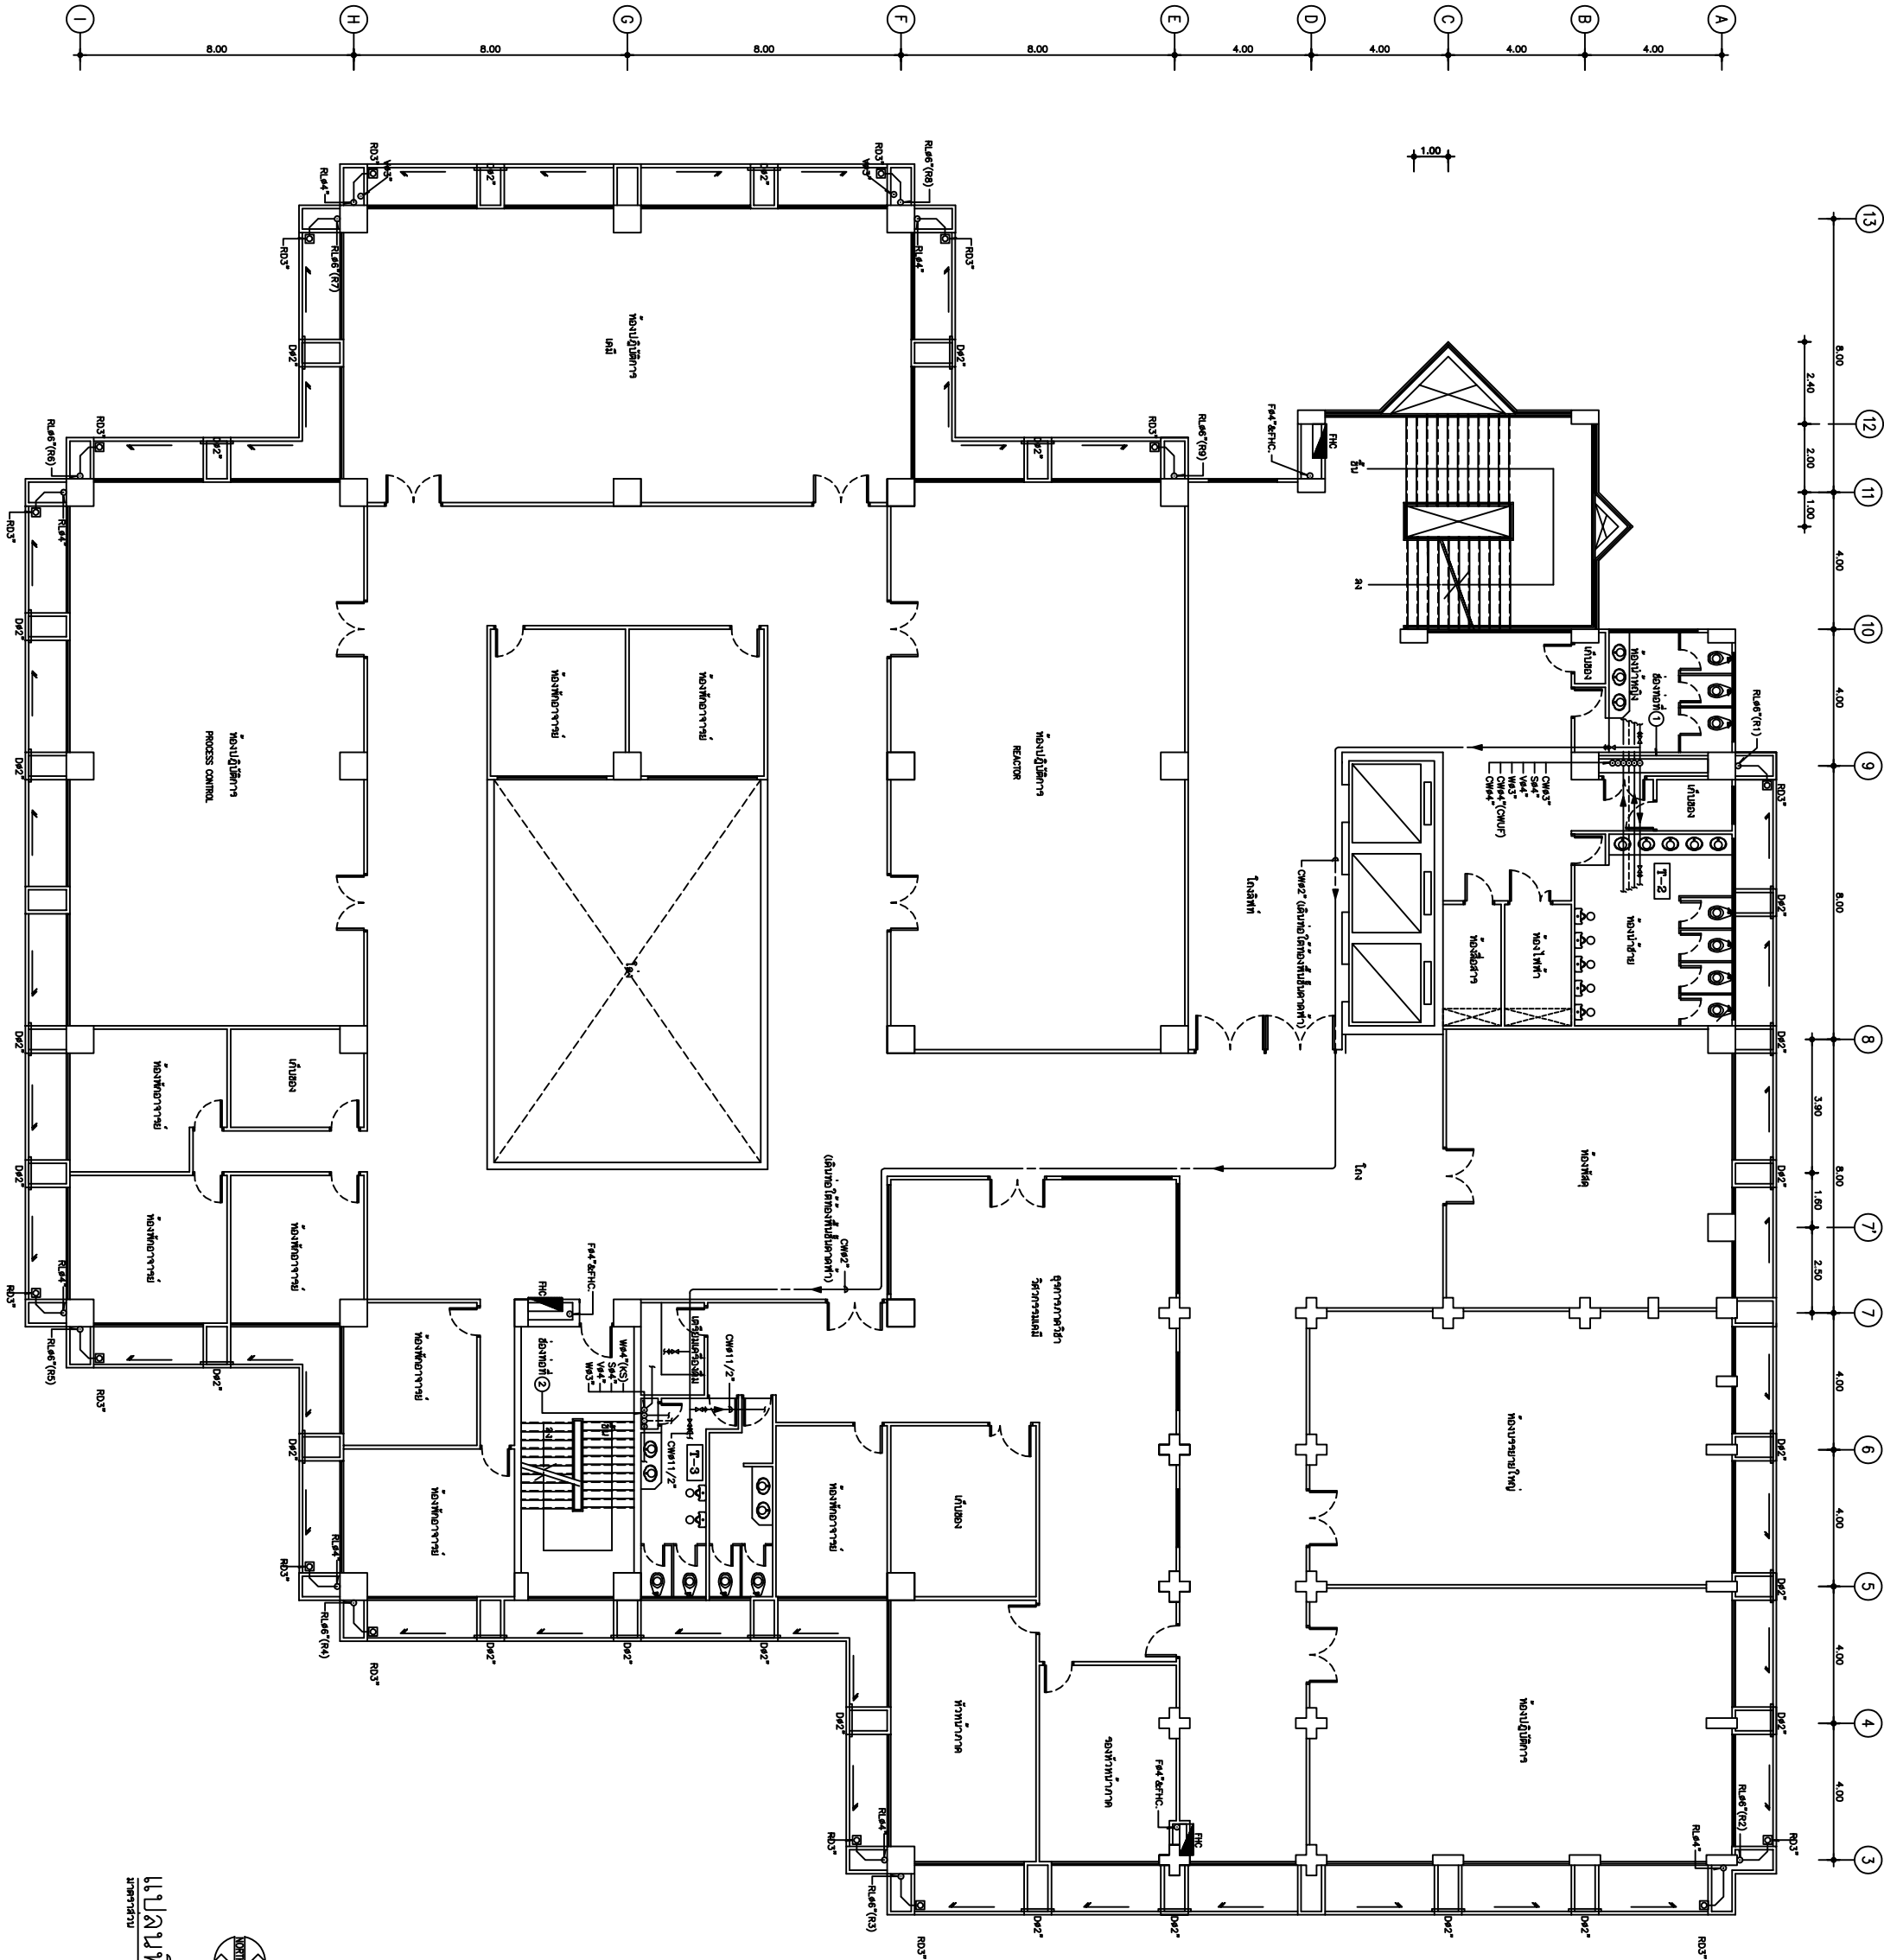

แปลนชั้น 8
1 : 100