

บริษัท เอ-สัน คอนสตรัคชั่น (ประเทศไทย) จำกัด
J-SONS CONSTRUCTION (THAILAND) COMPANY LIMITED
893/36-37 ถนนพหลโยธิน แขวงจตุจักร เขตจตุจักร กรุงเทพฯ 10130
Tel. (053) 214963 Fax. (053) 219842

ASBULT DRAWING

สถาปัตยวิศวกรรมและสิ่งแวดล้อม
คณะวิศวกรรมศาสตร
มหาวิทยาลัยเทคโนโลยีพระจอมเกล้าธนบุรี

OWNER

คณะวิศวกรรมศาสตร มหาวิทยาลัยเทคโนโลยีพระจอมเกล้าธนบุรี

ARCHITECTS

เขียน อธิพัฒน์ อดิเรก อดิเรก อดิเรก

STRUCTURAL ENGINEERS

เขียน อธิพัฒน์ อดิเรก อดิเรก อดิเรก

SANITARY ENGINEERS

เขียน อธิพัฒน์ อดิเรก อดิเรก อดิเรก

ELECTRICAL ENGINEERS

เขียน อธิพัฒน์ อดิเรก อดิเรก อดิเรก

MECHANICAL ENGINEERS

เขียน อธิพัฒน์ อดิเรก อดิเรก อดิเรก

DRAWN

เขียน อธิพัฒน์ อดิเรก อดิเรก อดิเรก

SHEET TITLE

แบบแปลนชั้นหลังคา

SCALE : 1 : 100


DATE : 9 กันยายน 2542

APPROVED :

DATE :

DRAWING NO. TOTAL SHEET

SN-16 26

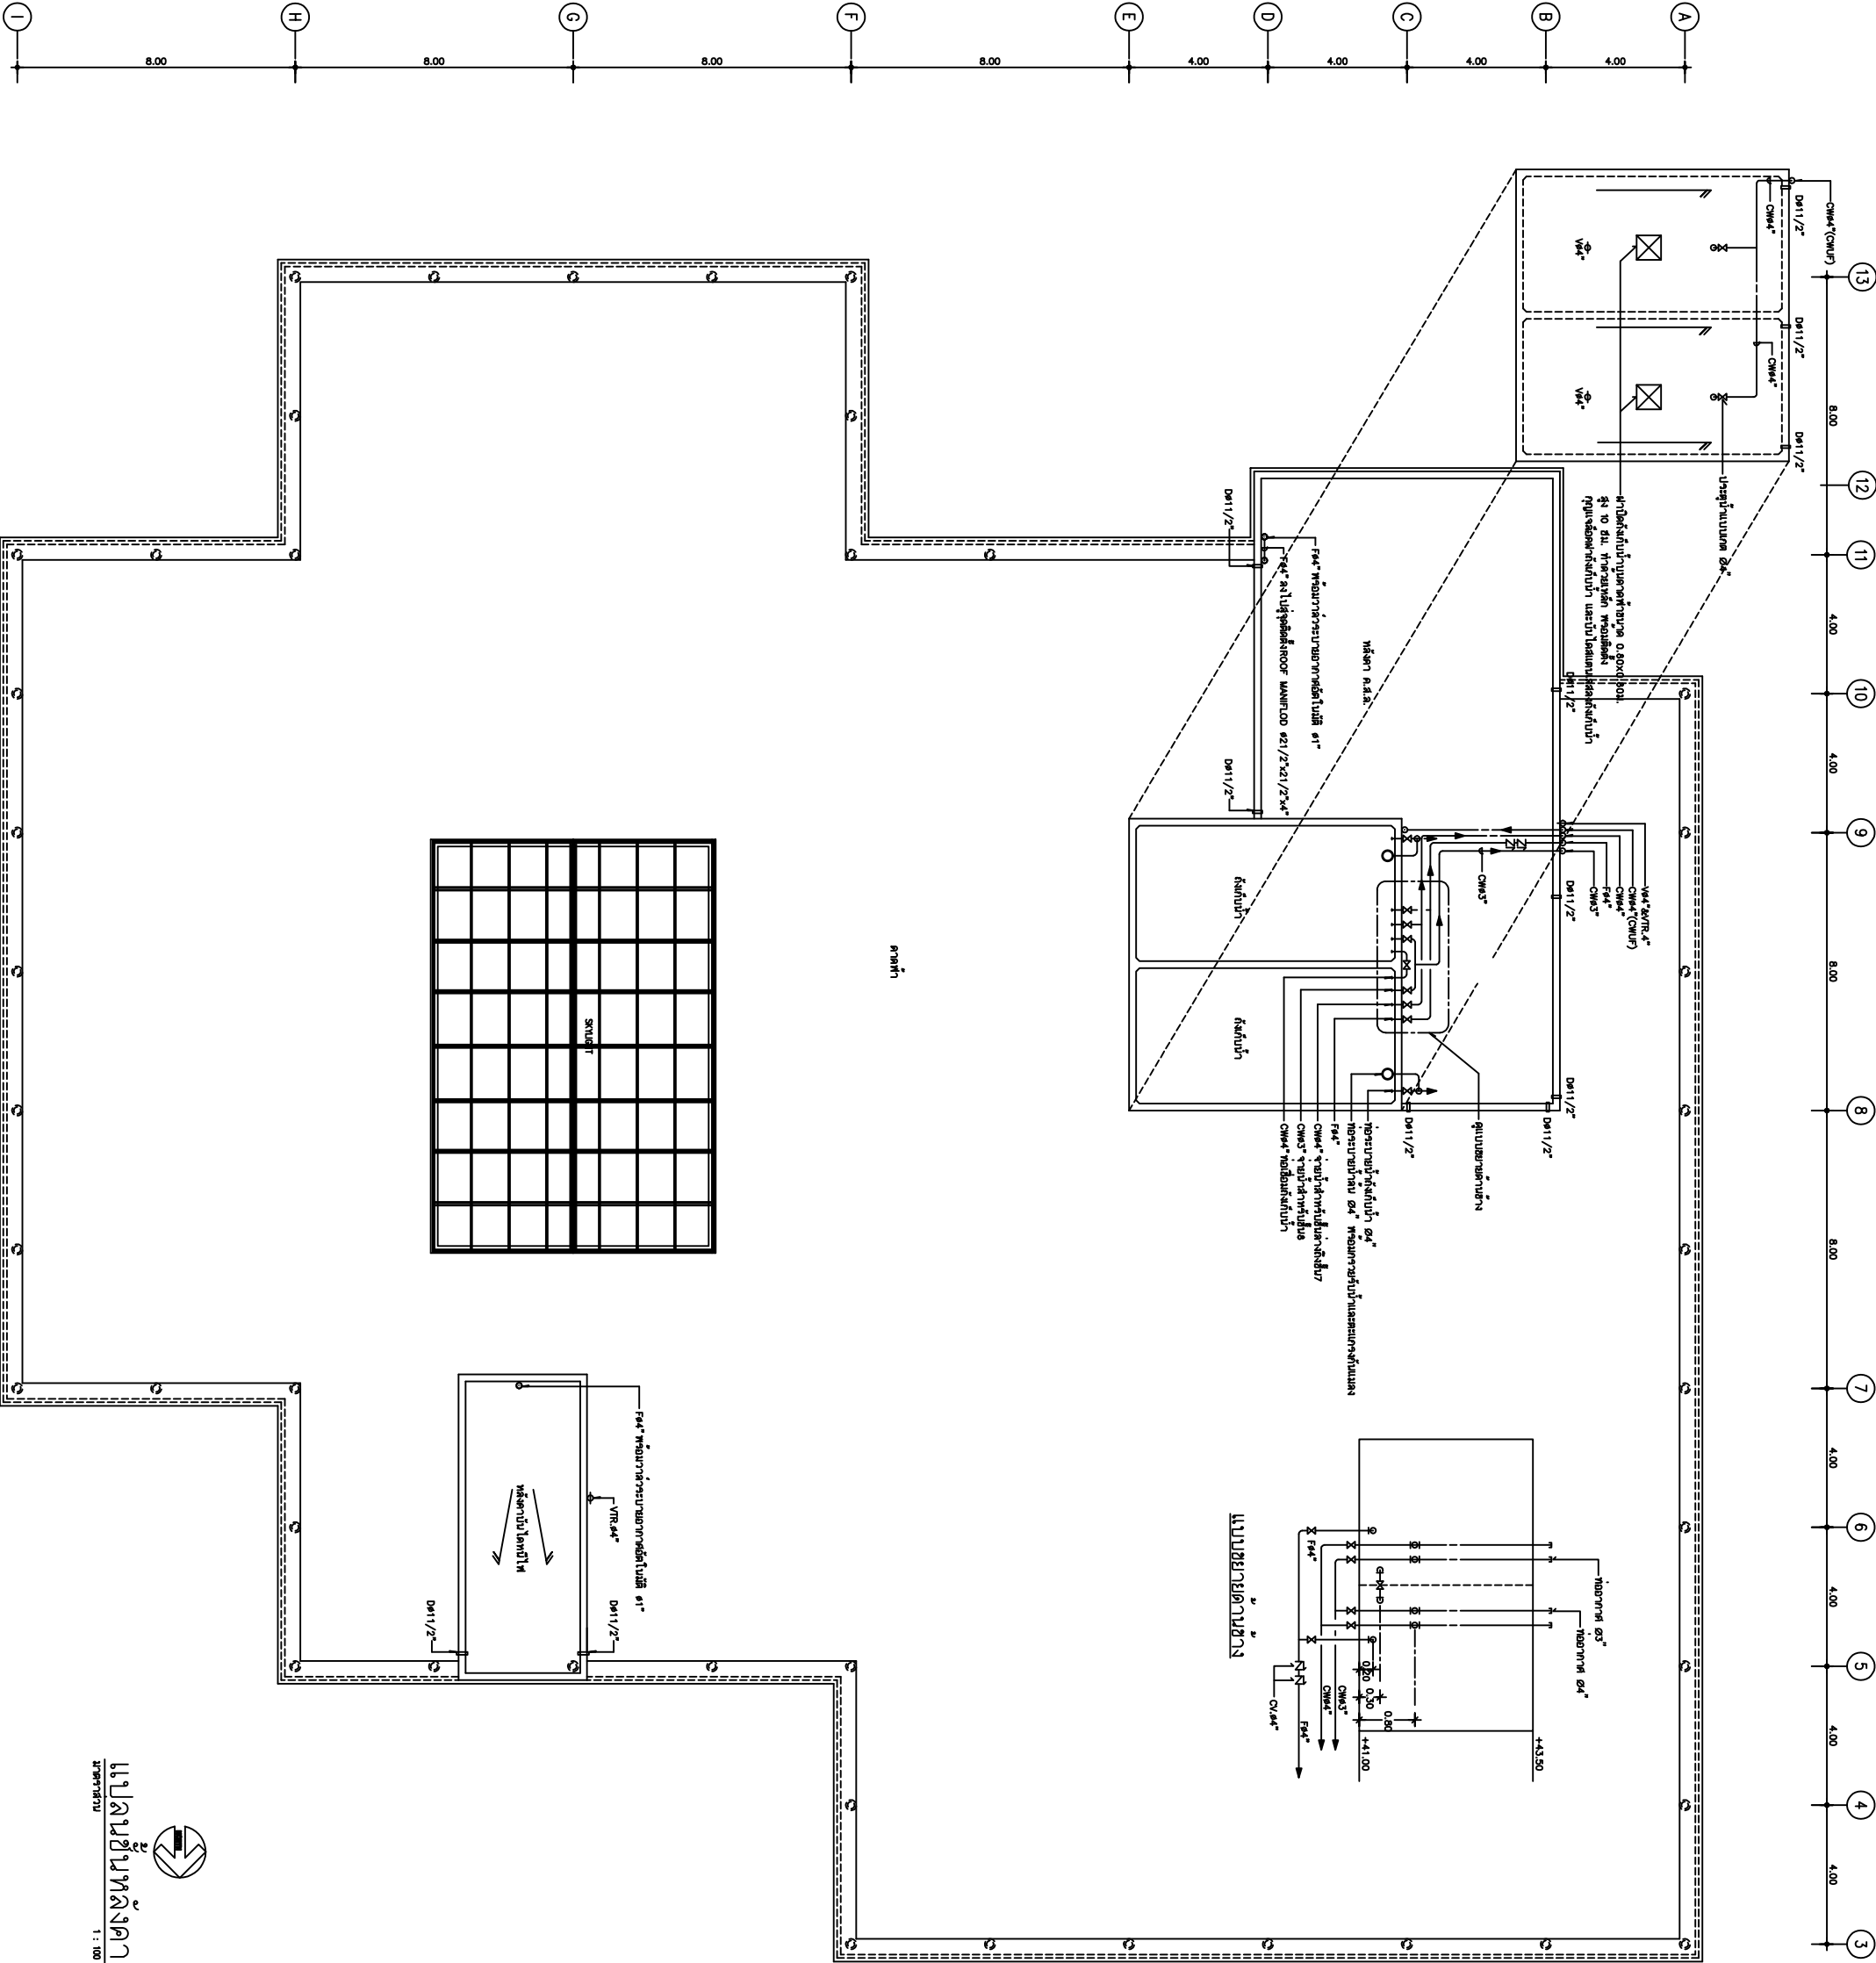

แปลนชั้นหลังคา
1 : 100